



Proposed Dual Occupancy

37 Osborne St Gerringong

Lot 90 D.P 241462

DRAWING LIST	
G-000	General Cover Sheet
G-099	Demolition Plan
G-100	General Site Plan
G-300	Site Waste Minimisation Plan
G-500	Shadow Diagrams
A-100	Site Analysis Plan
A-101	Torrens Title Plan
A-200	Garage Floor Plan
A-201	Ground Floor Plan
A-202	First Floor Plan
A-250	North Elevation
A-251	East Elevation
A-252	South Elevation
A-253	West Elevation
A-300	Roof Plan
A-400	Section 1



WINDOW SCHEDULE

No.	Size (W) X (H)	Head Height	Type
W01	2000 X 500	1400	Fixed
W02	870 X 1000	2700	Sliding - Obs.
W03	2000 X 500	1400	Fixed
W04	870 X 1000	2700	Sliding - Obs.
W05	1200 X 900	2400	Fixed - Obs.
W06	650 X 1200	2400	Sliding - Obs.
W07	2200 X 1450	2400	Sliding
W08	1600 X 900	2400	Sliding
W09	2200 X 1450	2400	Sliding
W10	2200 X 600	2400	Sliding
W11	2200 X 600	2400	Sliding
W12	2200 X 1450	2400	Sliding
W13	1600 X 900	2400	Sliding
W14	2200 X 1450	2400	Sliding
W15	650 X 1200	2400	Sliding - Obs.
W16	1200 X 900	2400	Fixed - Obs.

DOOR SCHEDULE

No.	Size (W) X (H)	Head Height	Type
D01	5770 X 2700	2700	Sliding
D02	5770 X 2700	2700	Sliding
D03	3200 X 2400	2400	Sliding
D04	1800 X 2400	2400	Sliding
D05	1800 X 2400	2400	Sliding
D06	3200 X 2400	2400	Sliding



BUILDING DESIGNER
Redson Group Pty. Ltd.
trading as 'Progenia'
Wollongong, NSW 2500
E: contactus@progenia.com.au
A.B.N 21 158 799 663



Do not scale drawings. Use figured dimensions only. Check and verify levels and dimensions on site prior to commencement of any work, the preparation of shop drawings or the fabrication of components.

This drawing is the copyright of Redson Group Pty. Ltd. (Progenia) and is protected under the Copy Right Act 1968. Do not alter, reduce or transmit in any form or by any means without the express permission of Redson Group Pty. Ltd. (Progenia).


CLIENT
Brett McCroary
PROJECT
Proposed Dual Occupancy
LOCATION
37 Osborne St Gerringong NSW
PROJECT NUMBER
#038.2020

REVISION
1
DRAWN BY
JL
DATE
02.07.21
Issued for DA

DESCRIPTION
General Cover Sheet

PAGE SCALE
NTS
PAGE SIZE
A3

G-000

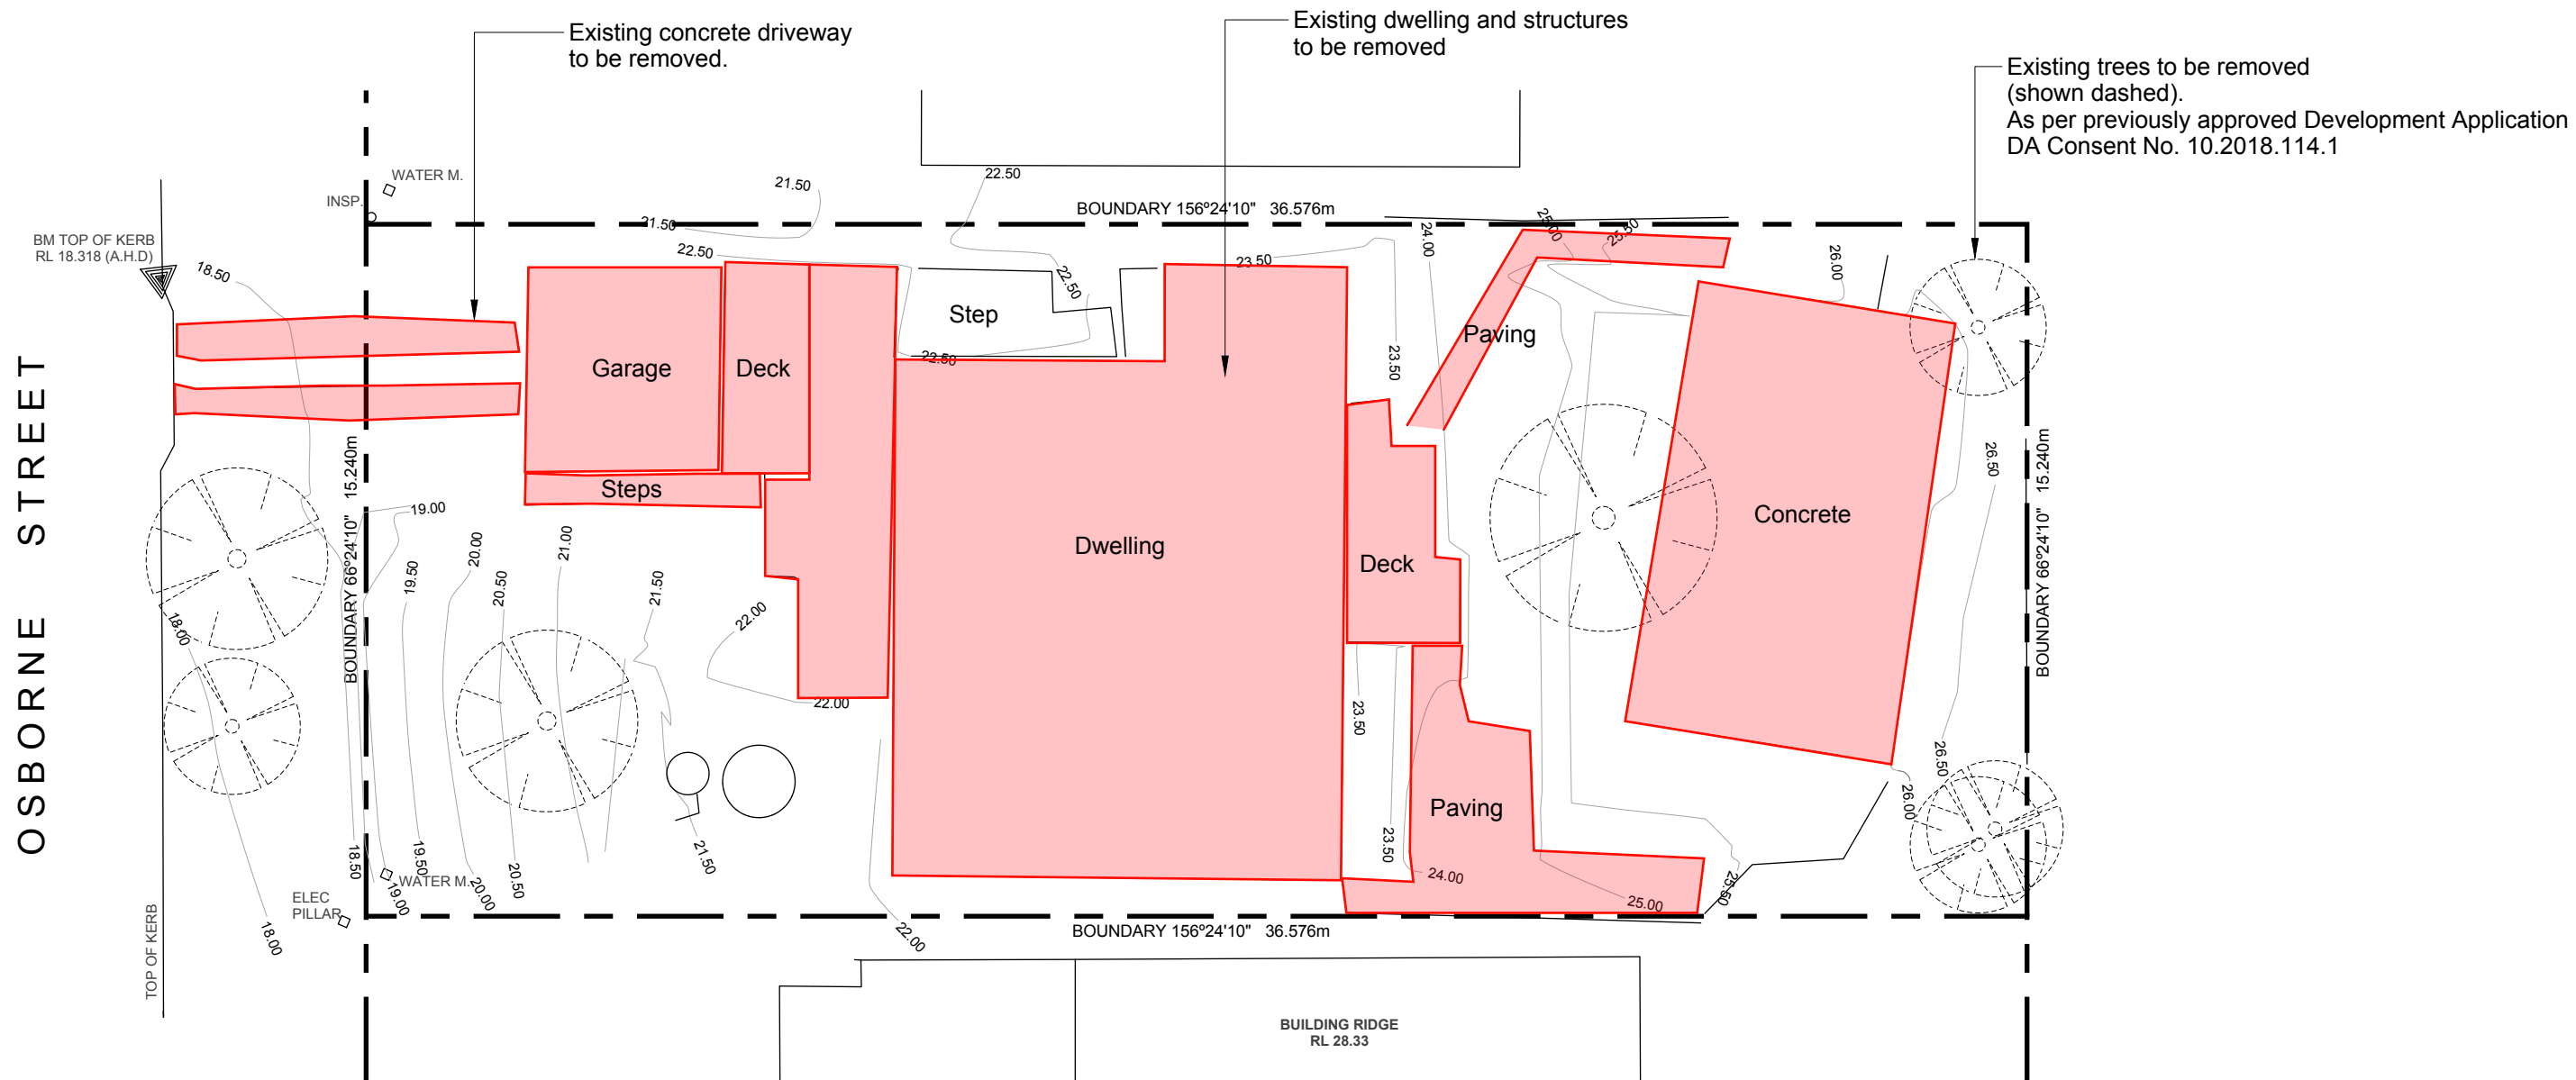

BUILDING DESIGNER
Redson Group Pty. Ltd.
trading as 'Progenia'
Wollongong, NSW 2500
E: contactus@progenia.com.au
A.B.N 21 158 799 663



Do not scale drawings. Use figured dimensions only. Check and verify levels and dimensions on site prior to commencement of any work, the preparation of shop drawings or the fabrication of components.

This drawing is the copyright of Redson Group Pty. Ltd. (Progenia) and is protected under the Copy Right Act 1968. Do not alter, reduce or transmit in any form or by any means without the express permission of Redson Group Pty. Ltd. (Progenia).

CLIENT
Brett McCroary

PROJECT
Proposed Dual Occupancy

LOCATION
37 Osborne St Gerringong NSW

PROJECT NUMBER
#038.2020


REVISION 1
DRAWN BY JL
DATE 02.07.21

DESCRIPTION
Demolition Plan

PAGE SCALE 1 : 150
PAGE SIZE A3

G-099

Issued for DA

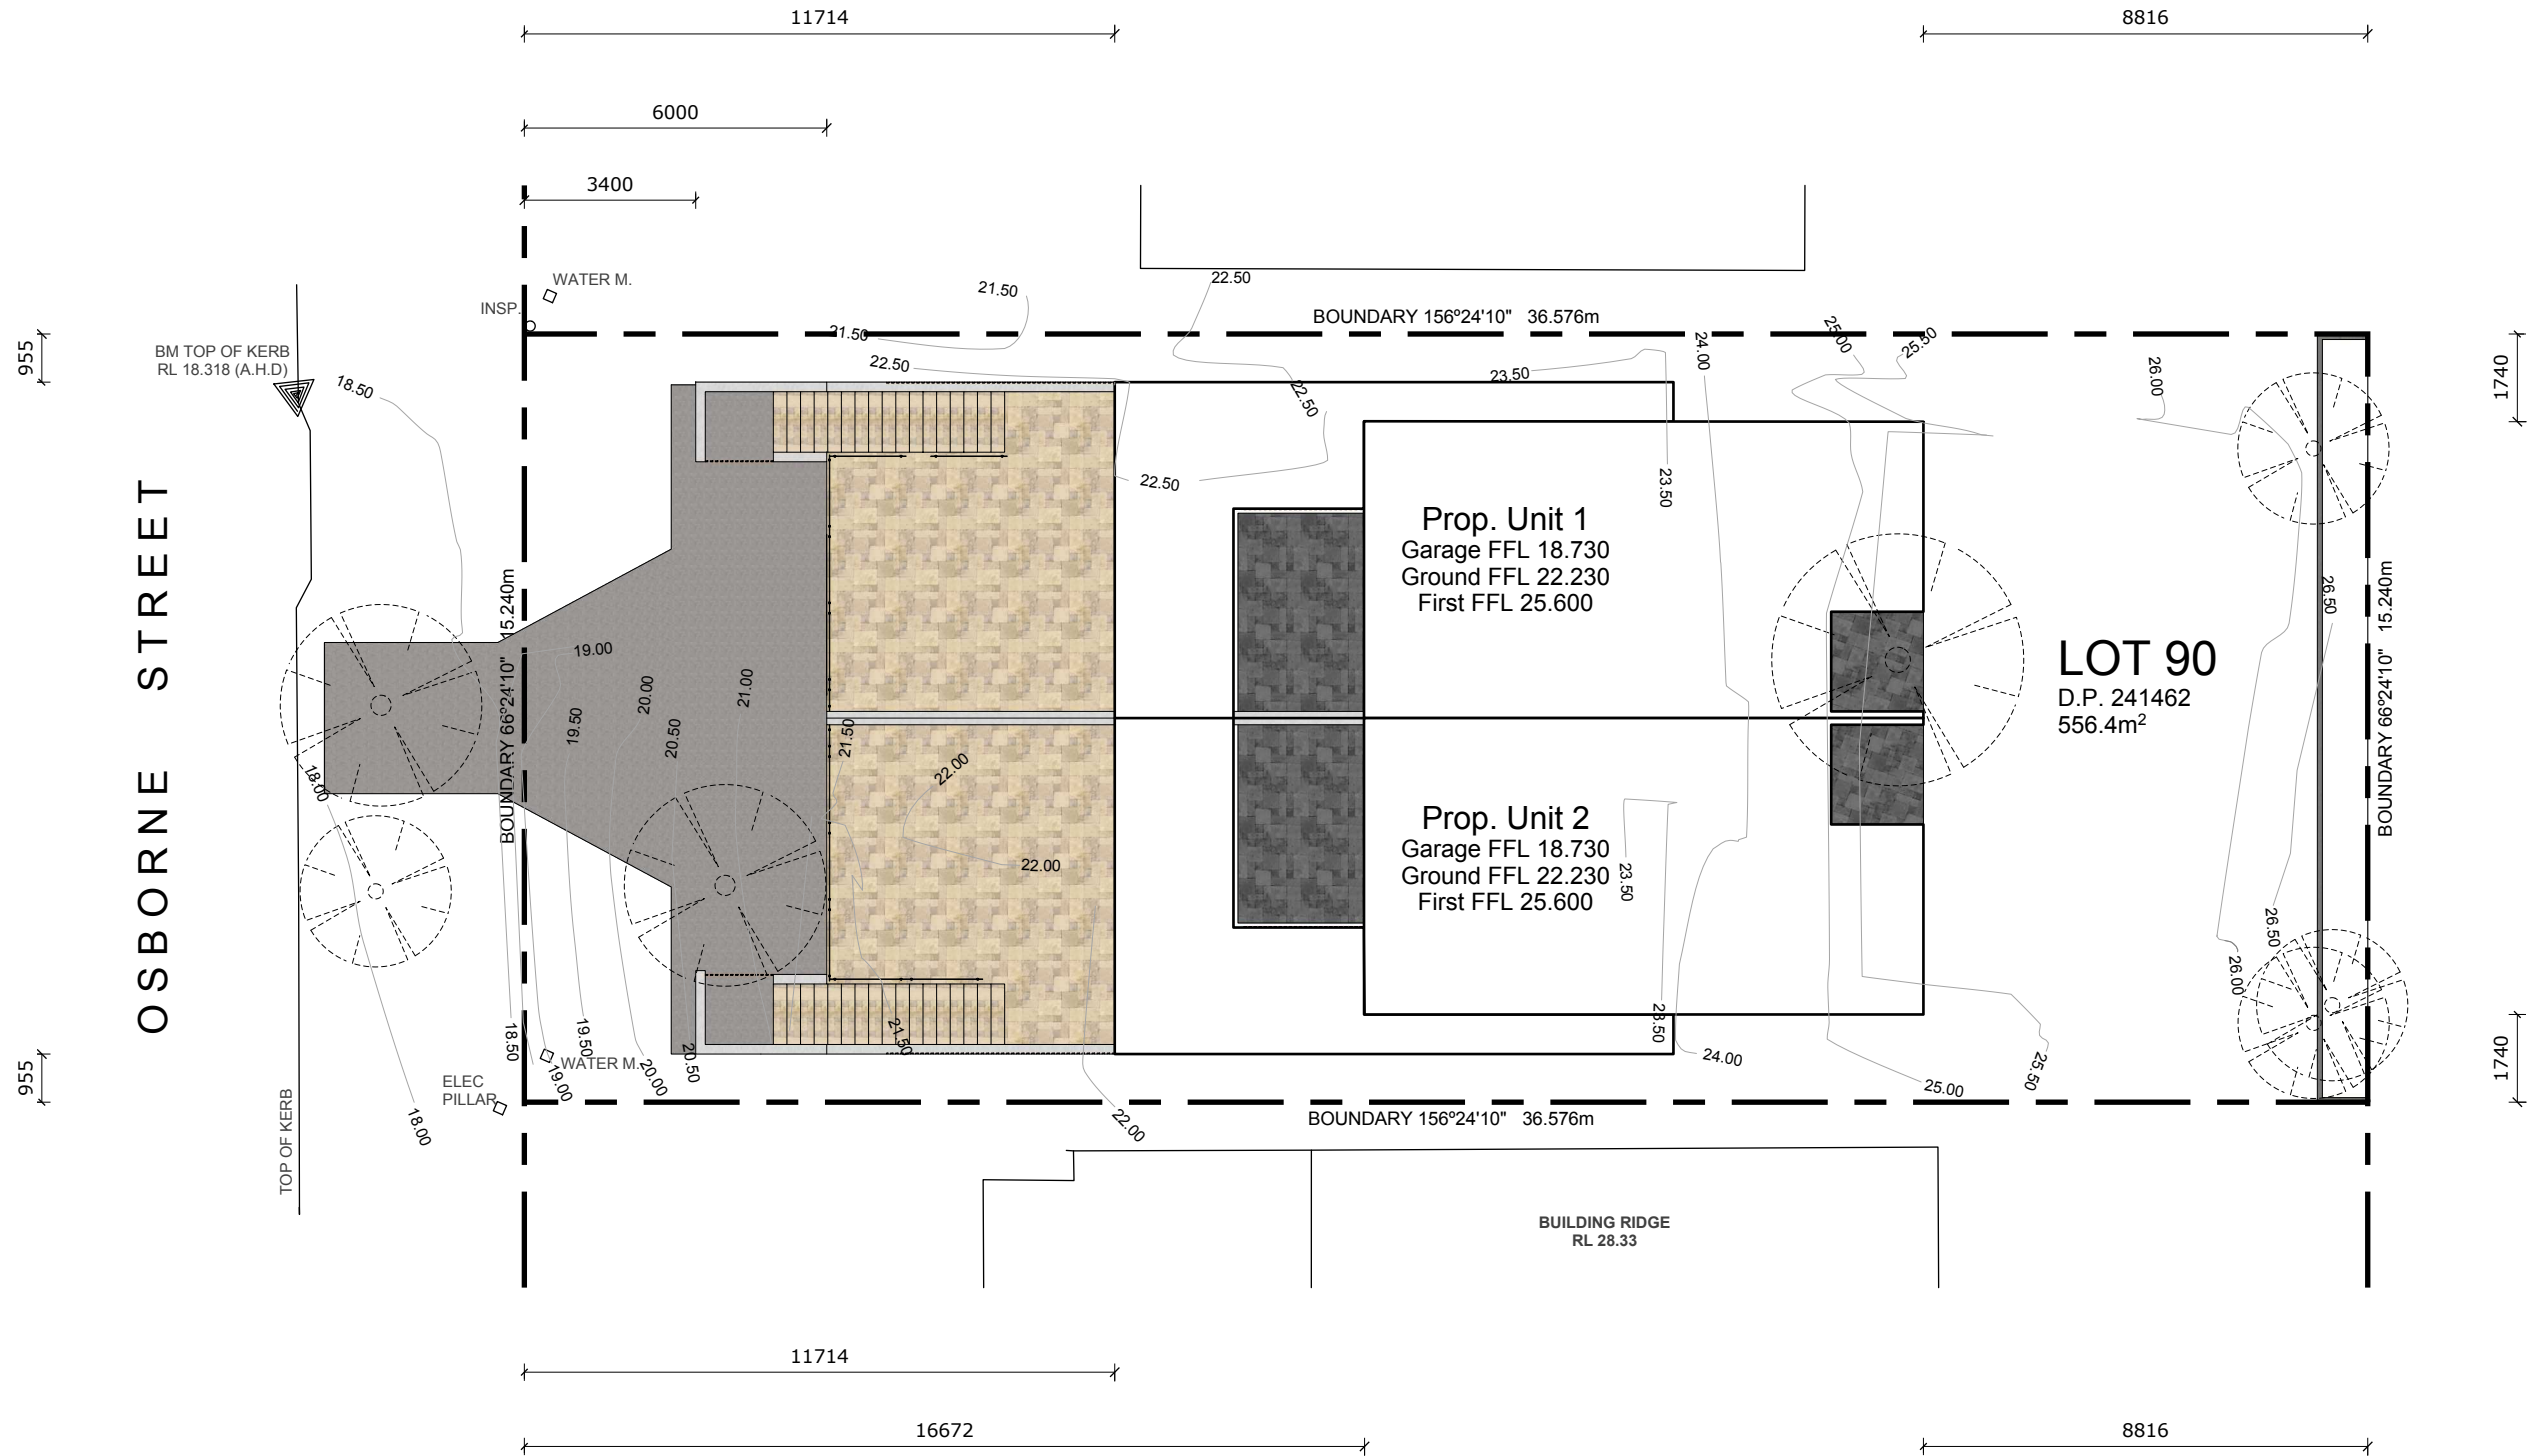

BUILDING DESIGNER
Redson Group Pty. Ltd.
trading as 'Progenia'
Wollongong, NSW 2500
E: contactus@progenia.com.au
A.B.N 21 158 799 663



Do not scale drawings. Use
figured dimensions only.
Check and verify levels and
dimensions on site prior to
commencement of any work,
the preparation of shop
drawings or the fabrication of
components.

This drawing is the copyright of
Redson Group Pty. Ltd. (Progenia) and
is protected under the Copy Right Act
1968. Do not alter, reduce or transmit in
any form or by any means without the
express permission of Redson Group
Pty. Ltd. (Progenia).

CLIENT
Brett McCroary
PROJECT
Proposed Dual Occupancy
LOCATION
37 Osborne St Gerringong NSW
PROJECT NUMBER
#038.2020


REVISION
1
DRAWN BY
JL
DATE
02.07.21


Issued for DA

DESCRIPTION
General Site Plan


PAGE SCALE
1 : 150
PAGE SIZE
A3

G-100

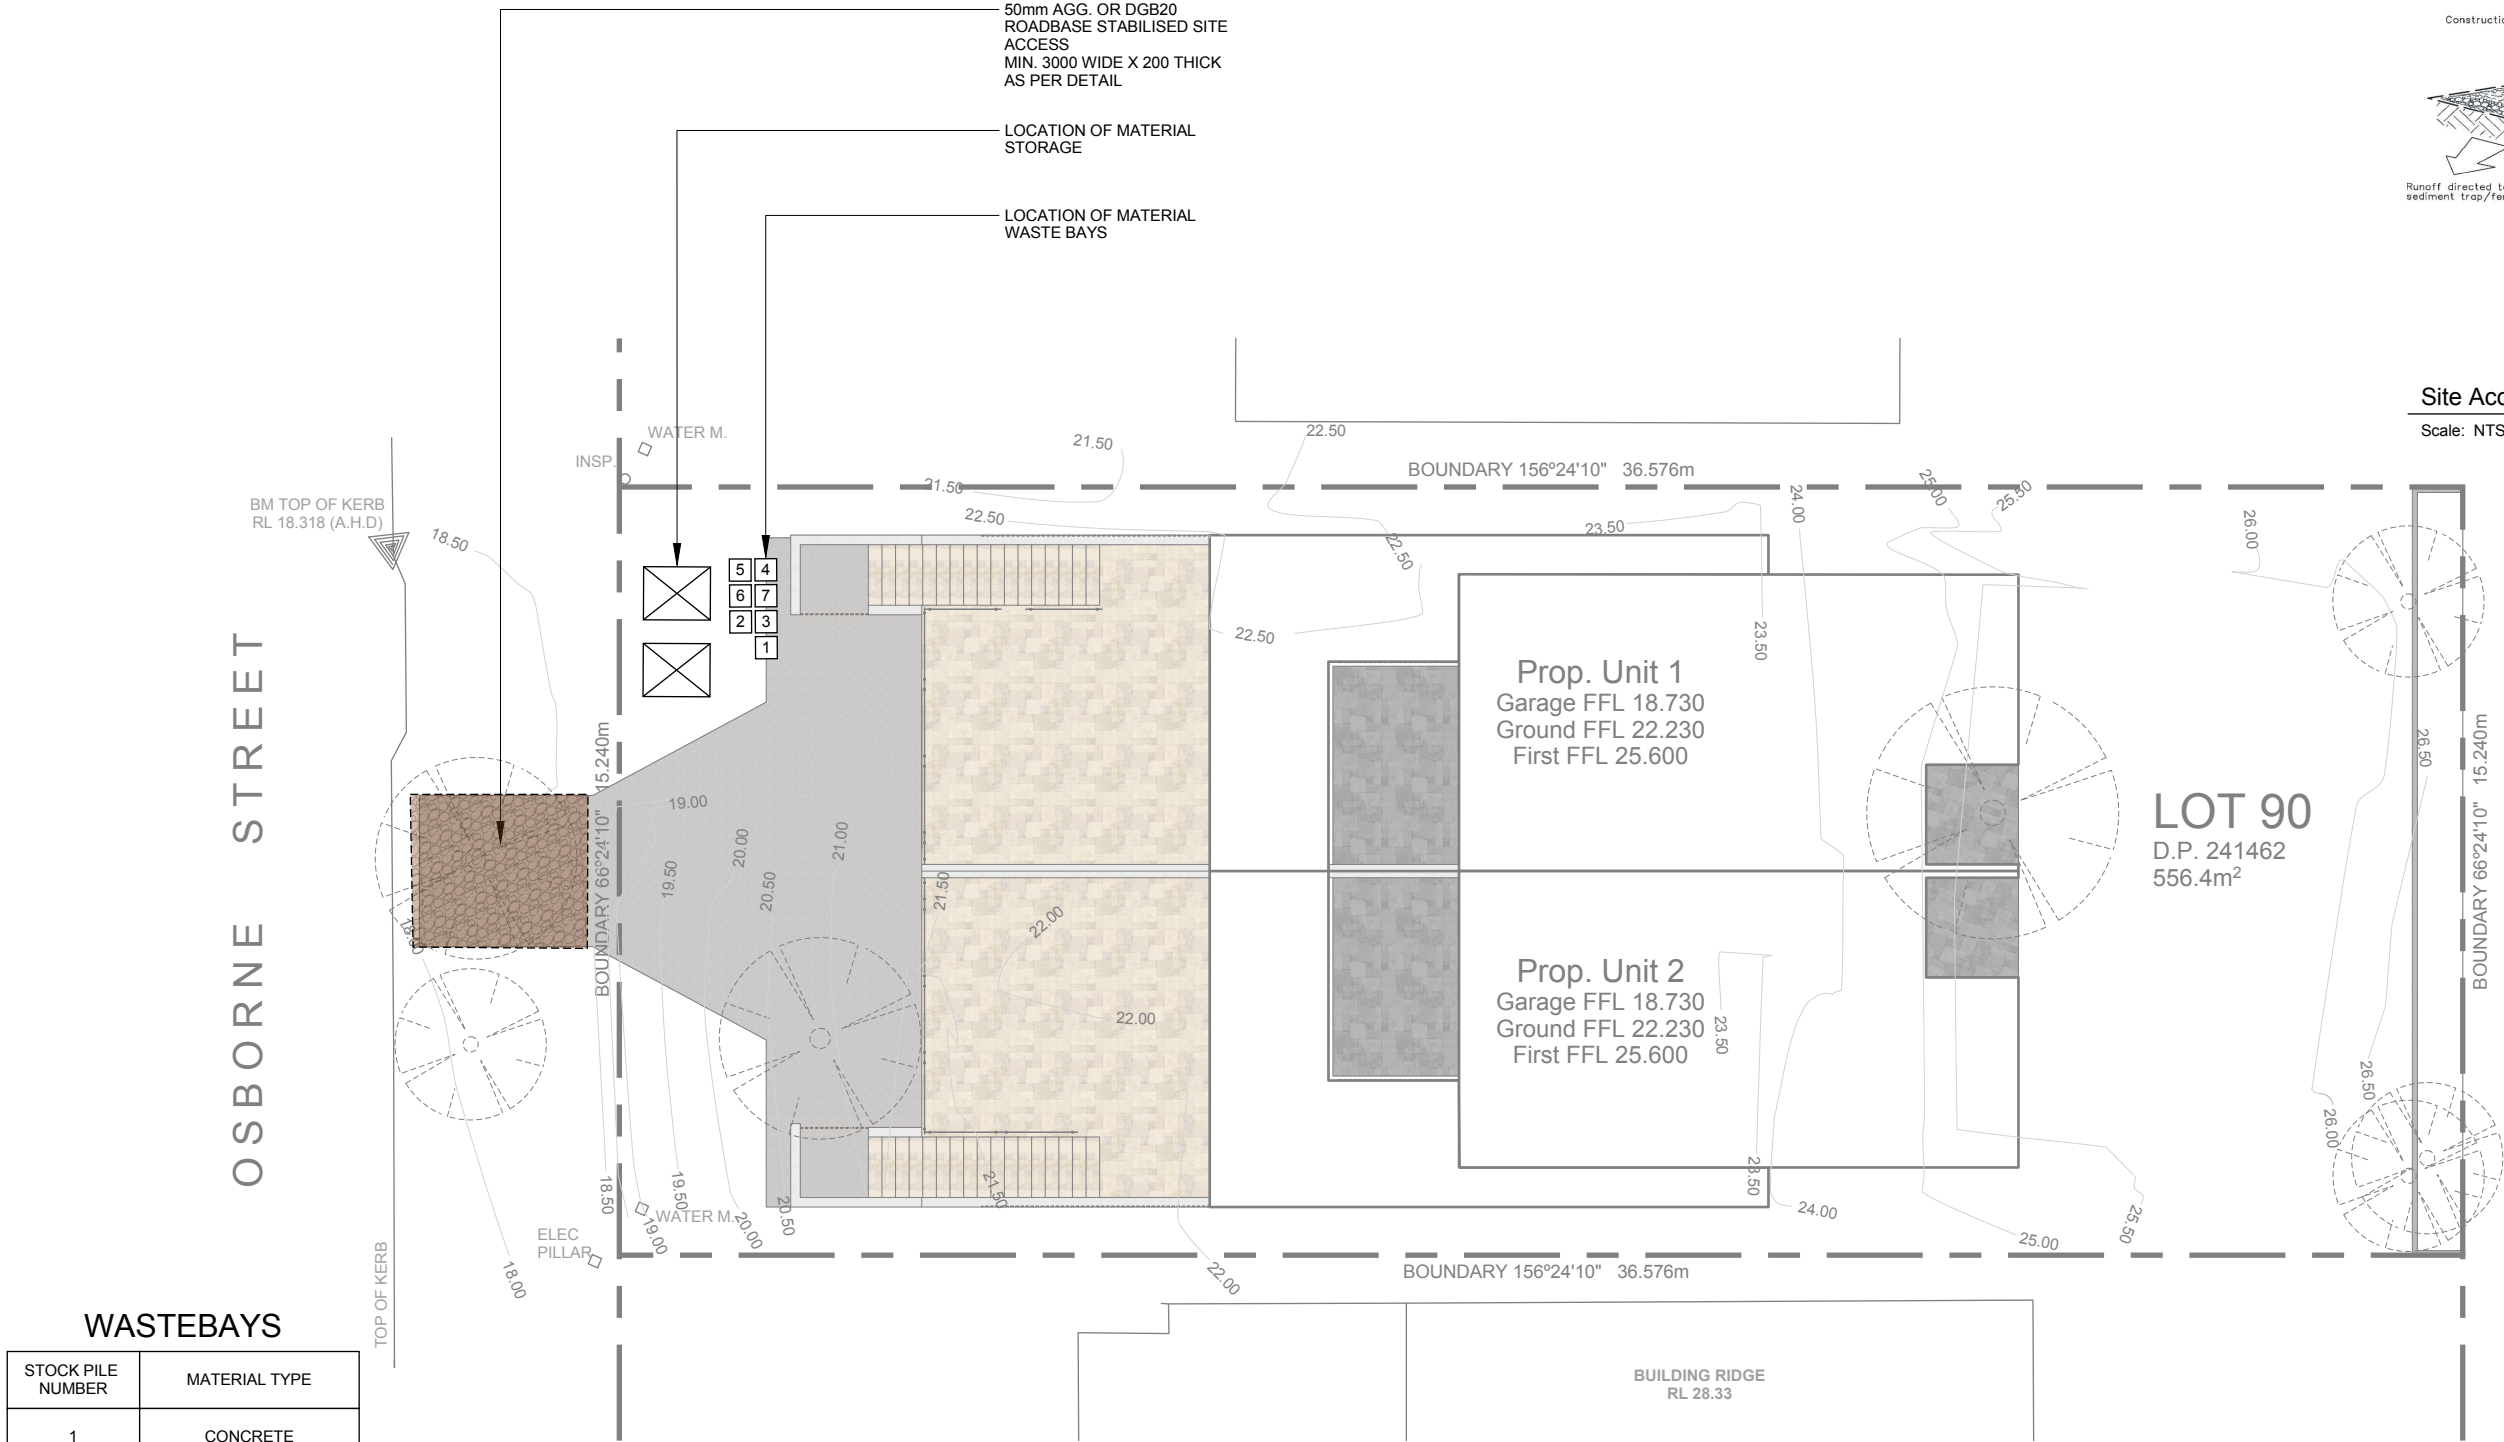

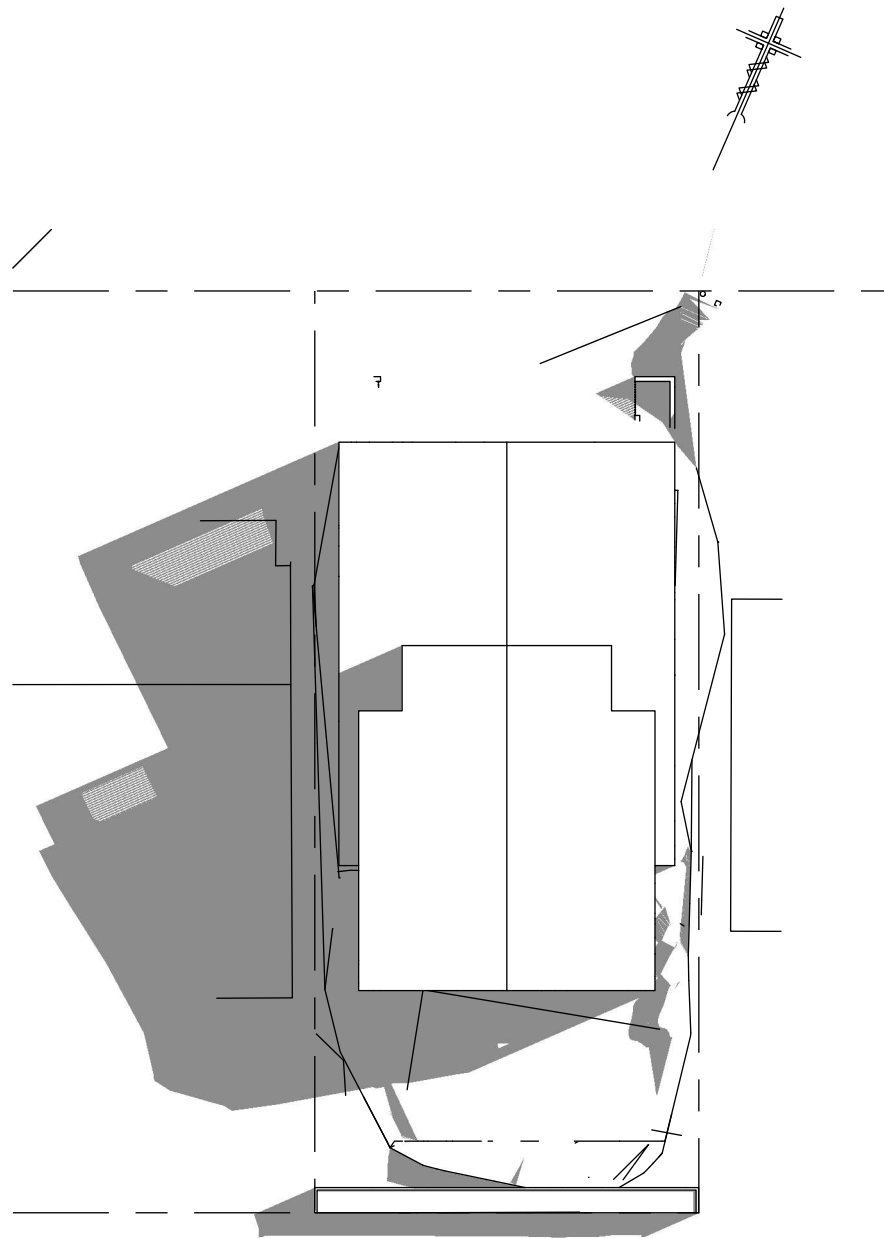

1 21 June - 9am
Scale: 1 : 300

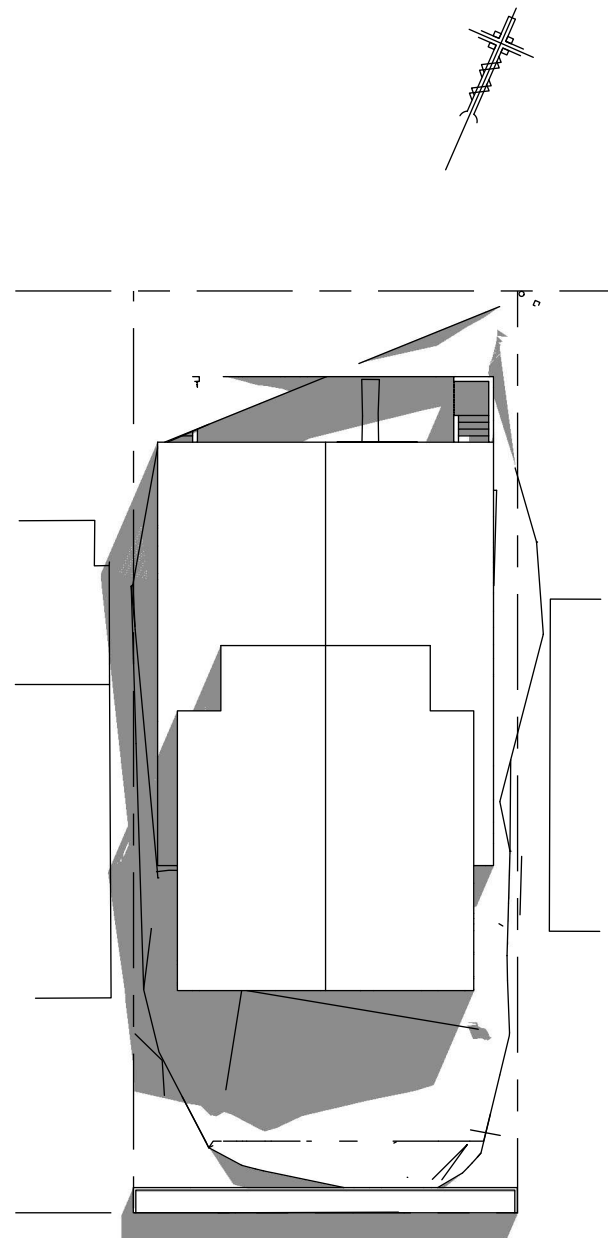

2 21 June - 12pm
Scale: 1 : 300



3 21 June - 3pm
Scale: 1 : 300

Floor Space Ratio (FSR)

Unit 2	
Ground Floor Area	66.12 sqm.
First Floor Area	54.01 sqm.
Garage	23.40 sqm.
Sub-Total Area	143.53 sqm.
Garage Allowance	-18 sqm.
Proposed Unit 1 Total	125.53 sqm.

Total Floor Space Area	251.06 sqm.
Land Area	561.30 sqm.
Calculated FSR	0.447



Do not scale drawings. Use figured dimensions only. Check and verify levels and dimensions on site prior to commencement of any work, the preparation of shop drawings or the fabrication of components.

This drawing is the copyright of Redson Group Pty. Ltd. (Progenia) and is protected under the Copy Right Act 1968. Do not alter, reduce or transmit in any form or by any means without the express permission of Redson Group Pty. Ltd. (Progenia).

CLIENT
Brett McCroary

PROJECT
Proposed Dual Occupancy

LOCATION
37 Osborne St Gerringong NSW

PROJECT NUMBER
#038.2020

REVISION	DRAWN BY	DATE
1	JL	02.07.21

Issued for DA

DESCRIPTION	Site Analysis Plan
-------------	--------------------

PAGE SCALE
1 : 150

PAGE SIZE
A3

A-100

Floor Space Ratio (FSR)

Unit 2	
Ground Floor Area	66.12 sqm.
First Floor Area	54.01 sqm.
Garage	23.40 sqm.
Sub-Total Area	143.53 sqm.
Garage Allowance	-18 sqm.
Proposed Unit 1 Total	125.53 sqm.

Total Floor Space Area	251.06 sqm.
Land Area	561.30 sqm.
Calculated FSR	0.447



Do not scale drawings. Use figured dimensions only. Check and verify levels and dimensions on site prior to commencement of any work, the preparation of shop drawings or the fabrication of components.

This drawing is the copyright of Redson Group Pty. Ltd. (Progenia) and is protected under the Copy Right Act 1968. Do not alter, reduce or transmit in any form or by any means without the express permission of Redson Group Pty. Ltd. (Progenia).

CLIENT
Brett McCroary

PROJECT
Proposed Dual Occupancy

LOCATION
37 Osborne St Gerringong NSW

PROJECT NUMBER
#038.2020

REVISION	DRAWN BY	DATE
1	JL	02.07.21




Issued for DA

DESCRIPTION	Torrens Title Plan
-------------	--------------------

PAGE SCALE
1 : 150

PAGE SIZE
A3

A-101

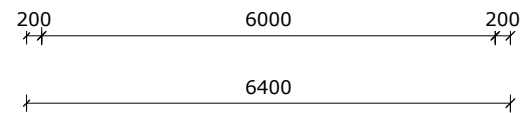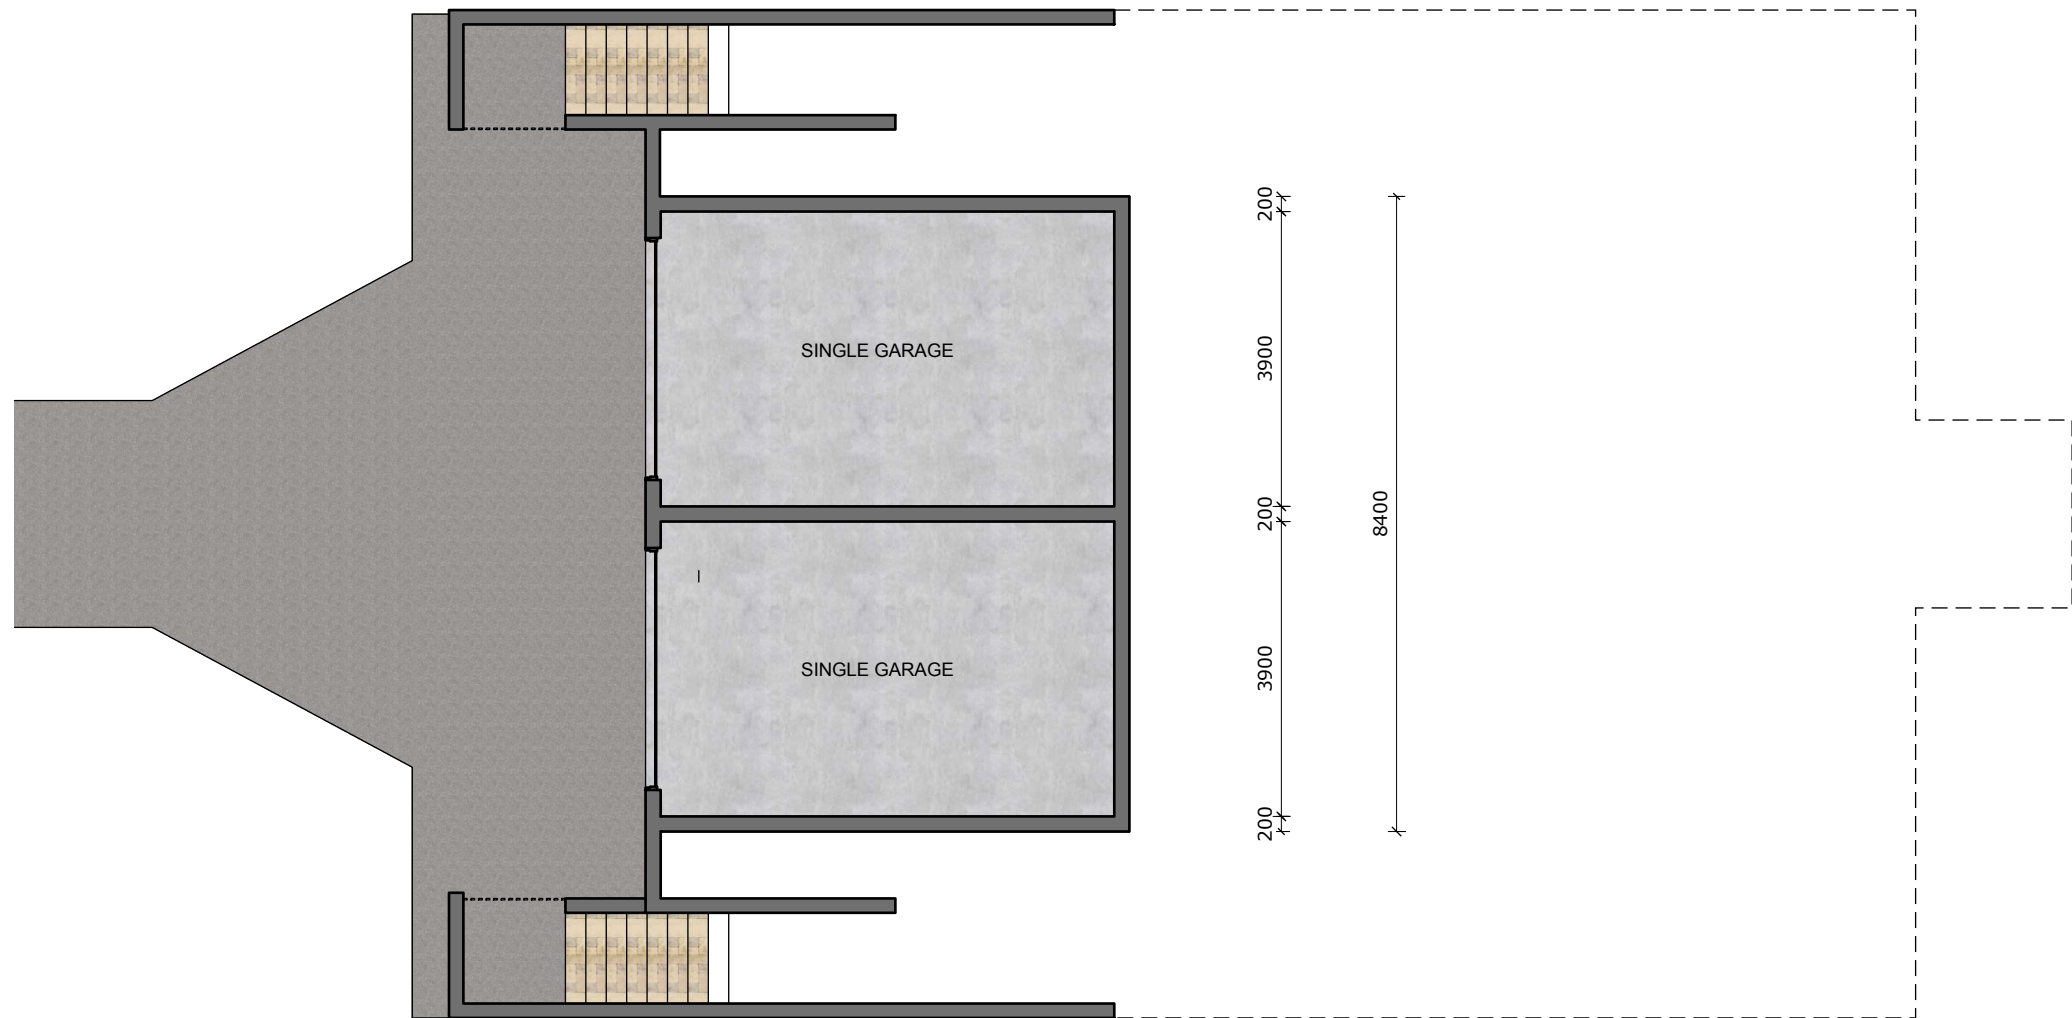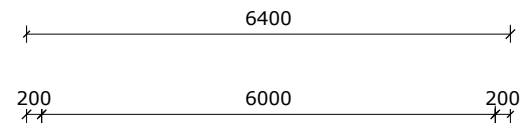

BUILDING DESIGNER
Redson Group Pty. Ltd.
trading as 'Progenia'
Wollongong, NSW 2500
E: contactus@progenia.com.au
A.B.N 21 158 799 663



Do not scale drawings. Use figured dimensions only. Check and verify levels and dimensions on site prior to commencement of any work, the preparation of shop drawings or the fabrication of components.

This drawing is the copyright of Redson Group Pty. Ltd. (Progenia) and is protected under the Copy Right Act 1968. Do not alter, reduce or transmit in any form or by any means without the express permission of Redson Group Pty. Ltd. (Progenia).

CLIENT
Brett McCroary
PROJECT
Proposed Dual Occupancy
LOCATION
37 Osborne St Gerringong NSW
PROJECT NUMBER
#038.2020

REVISION	DRAWN BY	DATE
1	JL	02.07.21


Issued for DA


DESCRIPTION
Garage Floor Level

PAGE SCALE	PAGE SIZE
1 : 100	A3


A-200



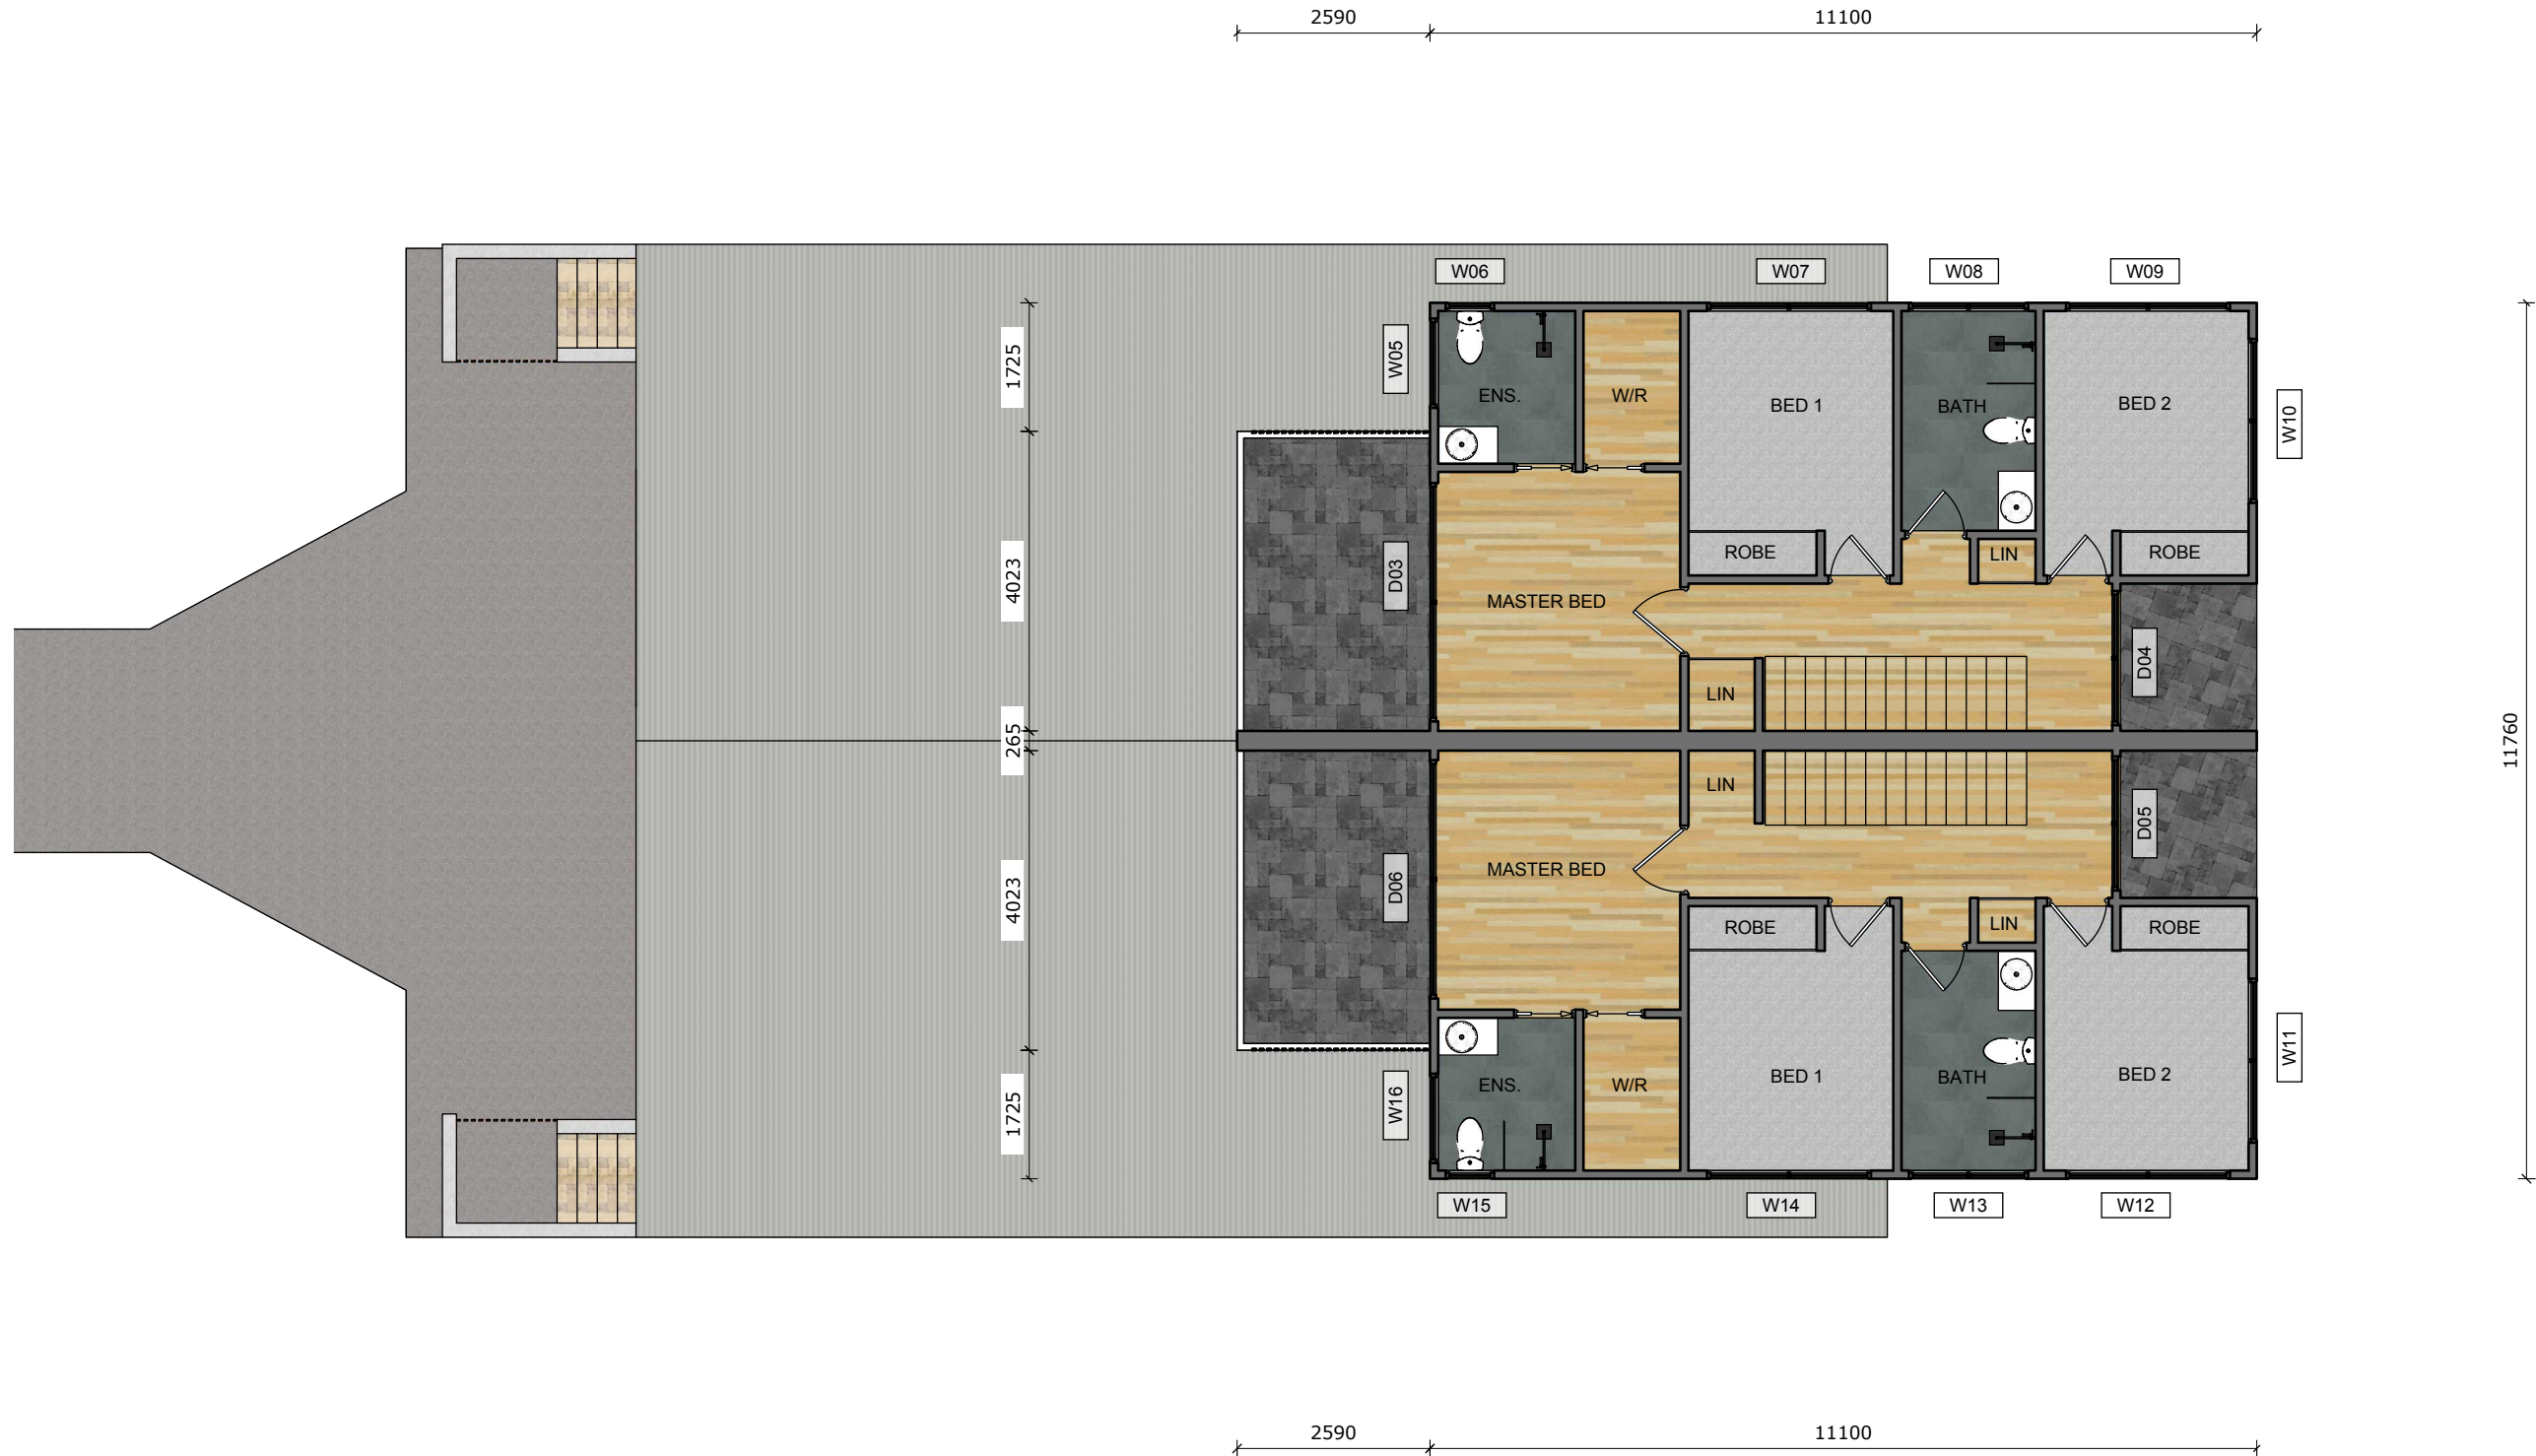


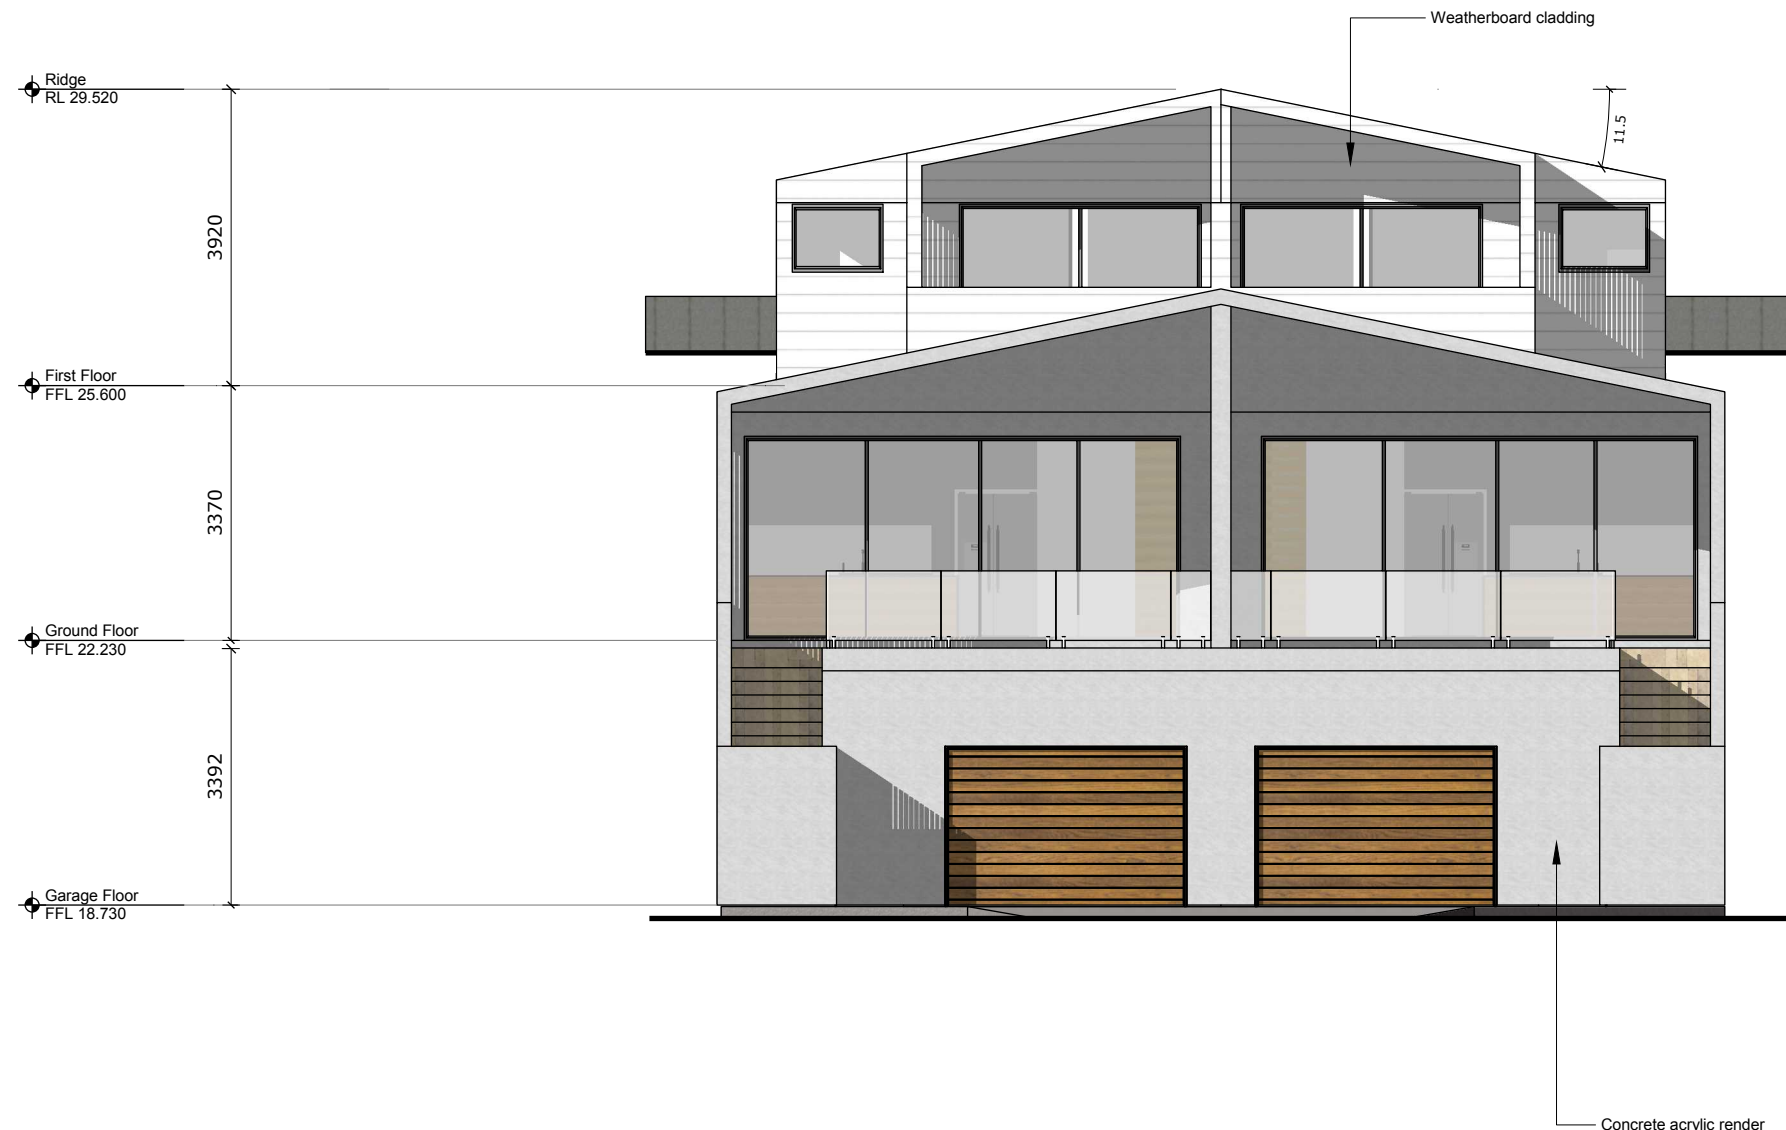


1 North Elevation
Scale: 1 : 100

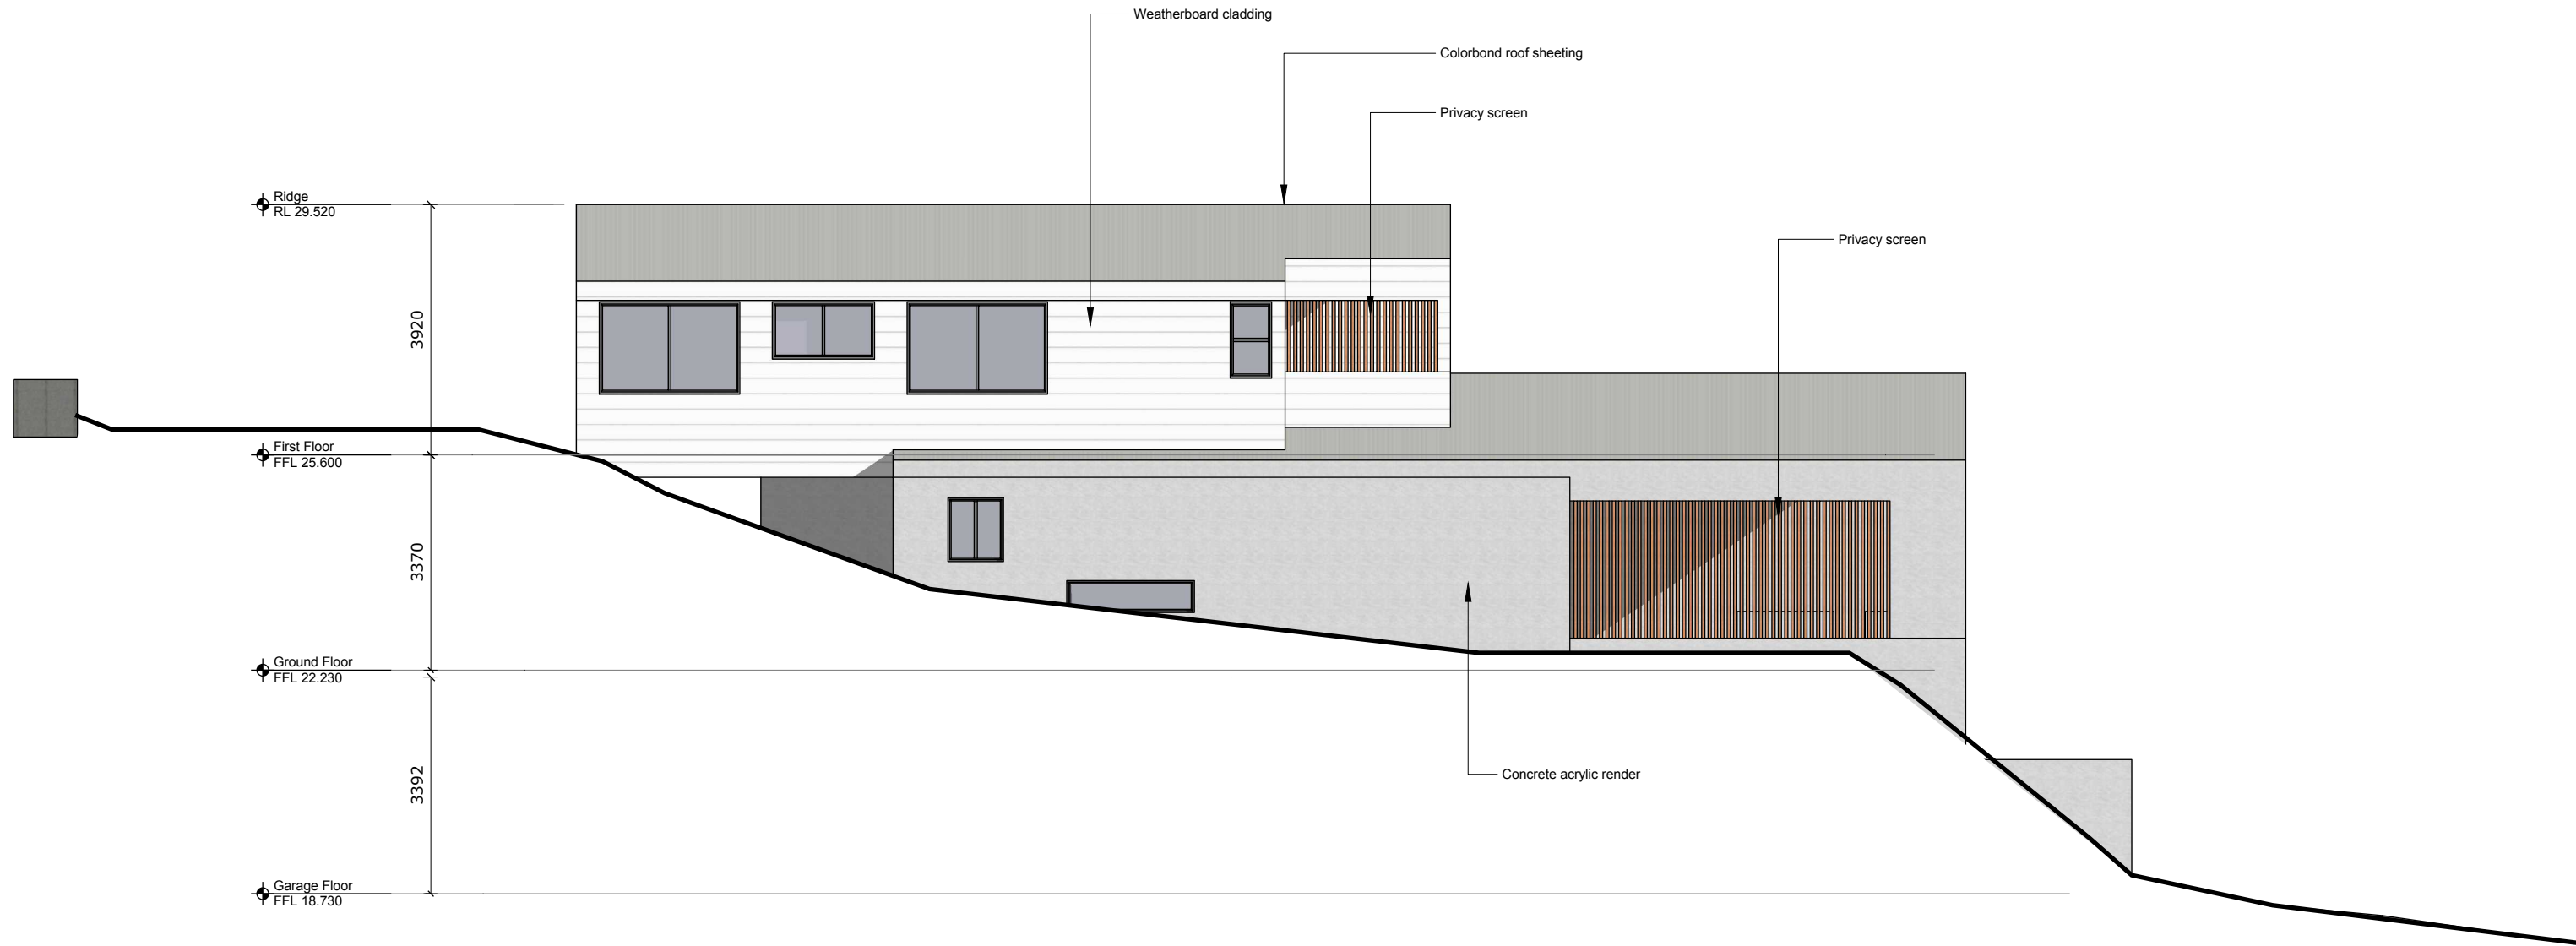


2 East Elevation
Scale: 1 : 100

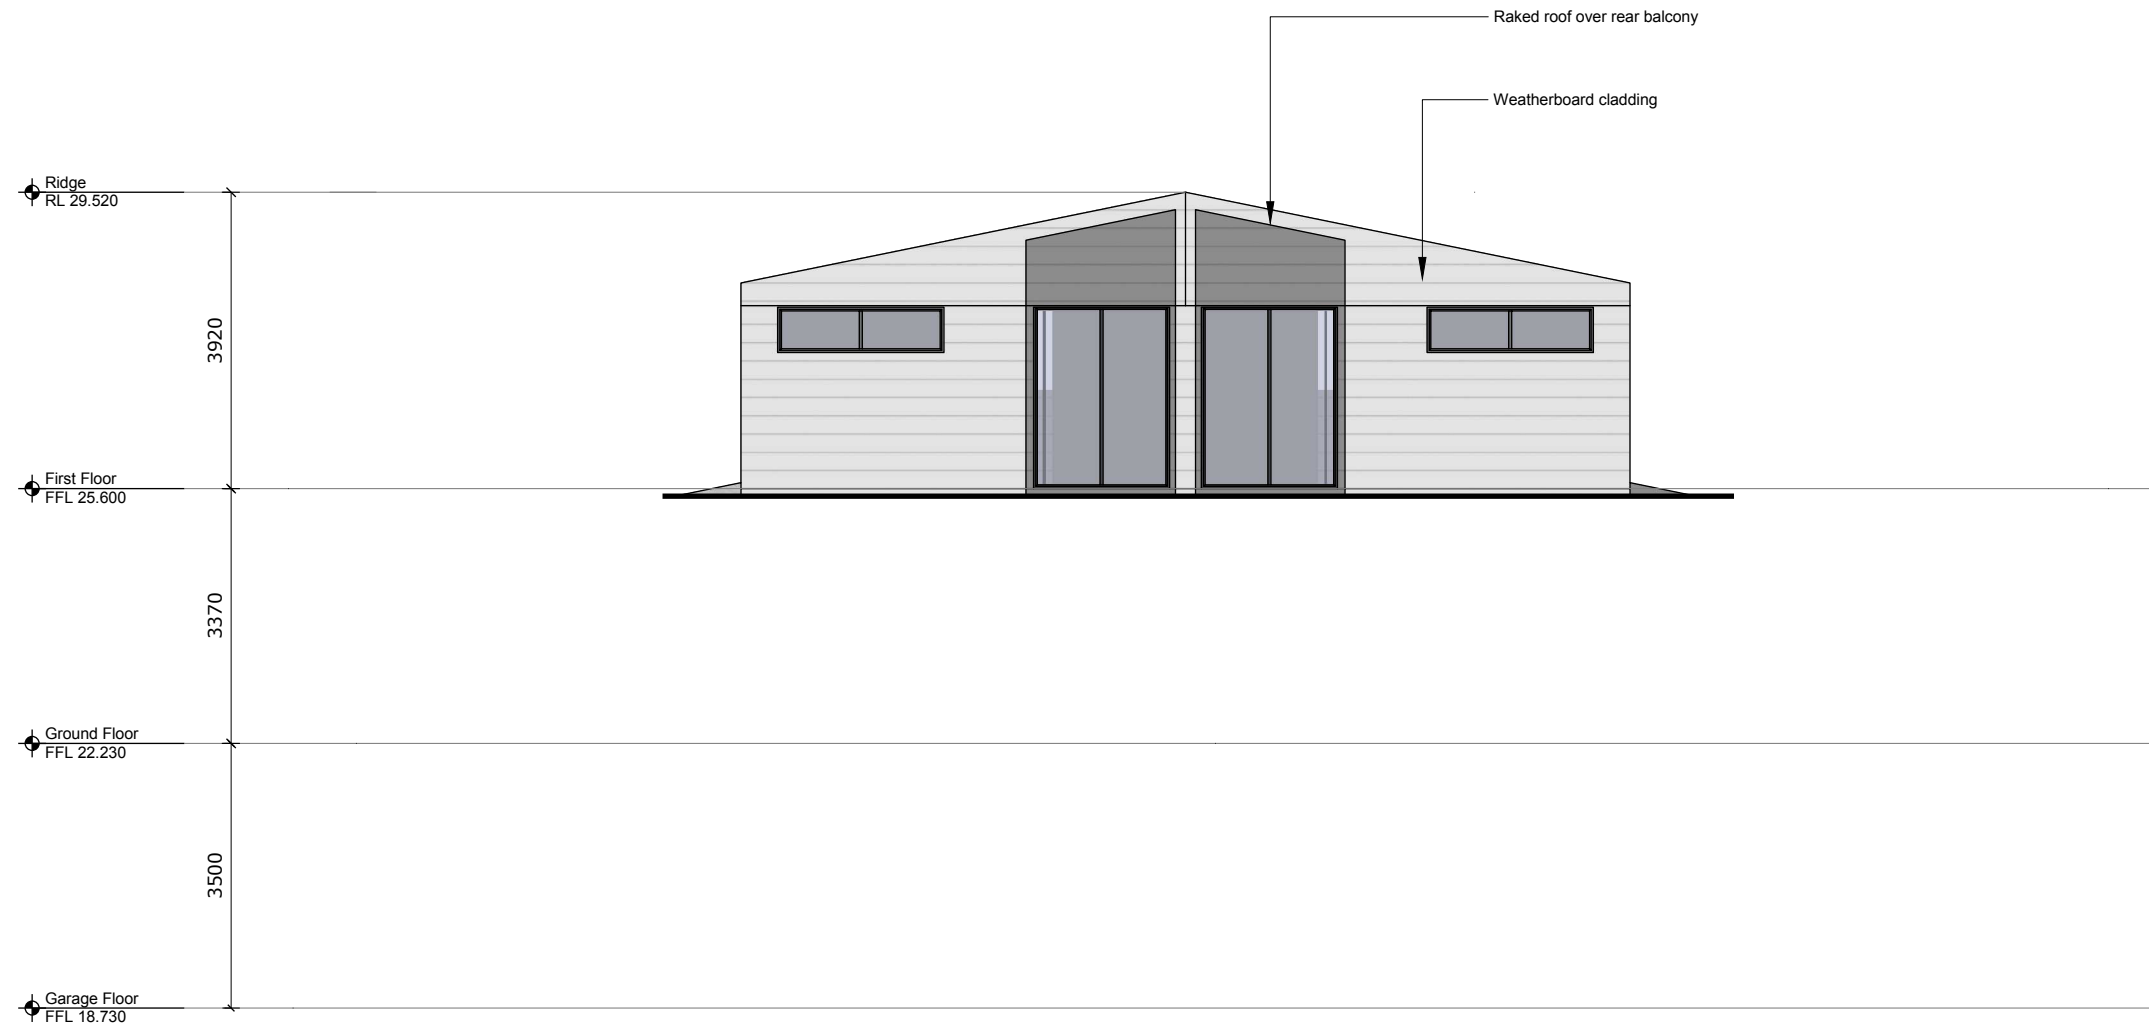

3 South Elevation
Scale: 1 : 100

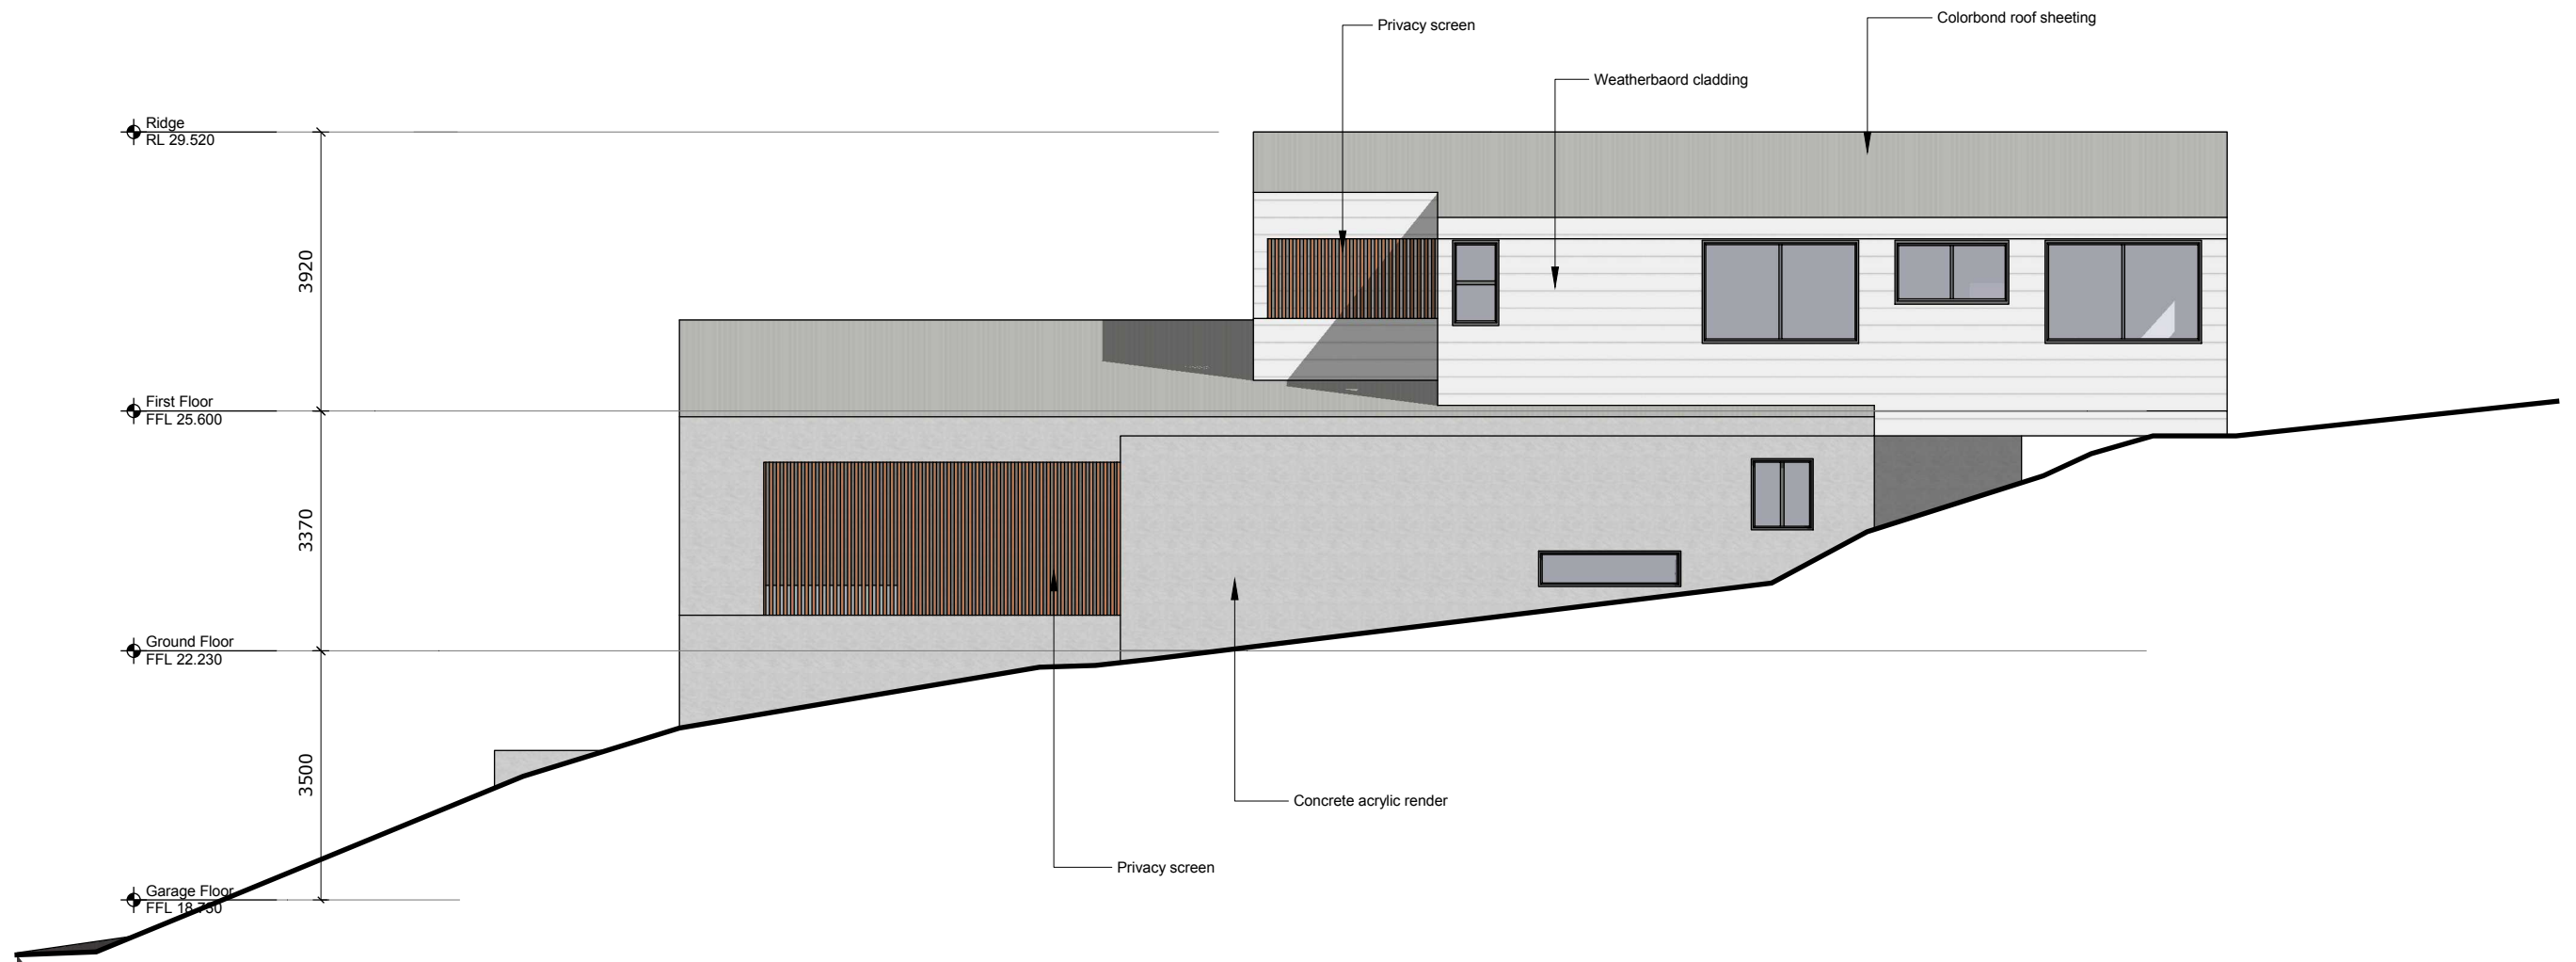

4 West Elevation
Scale: 1 : 100

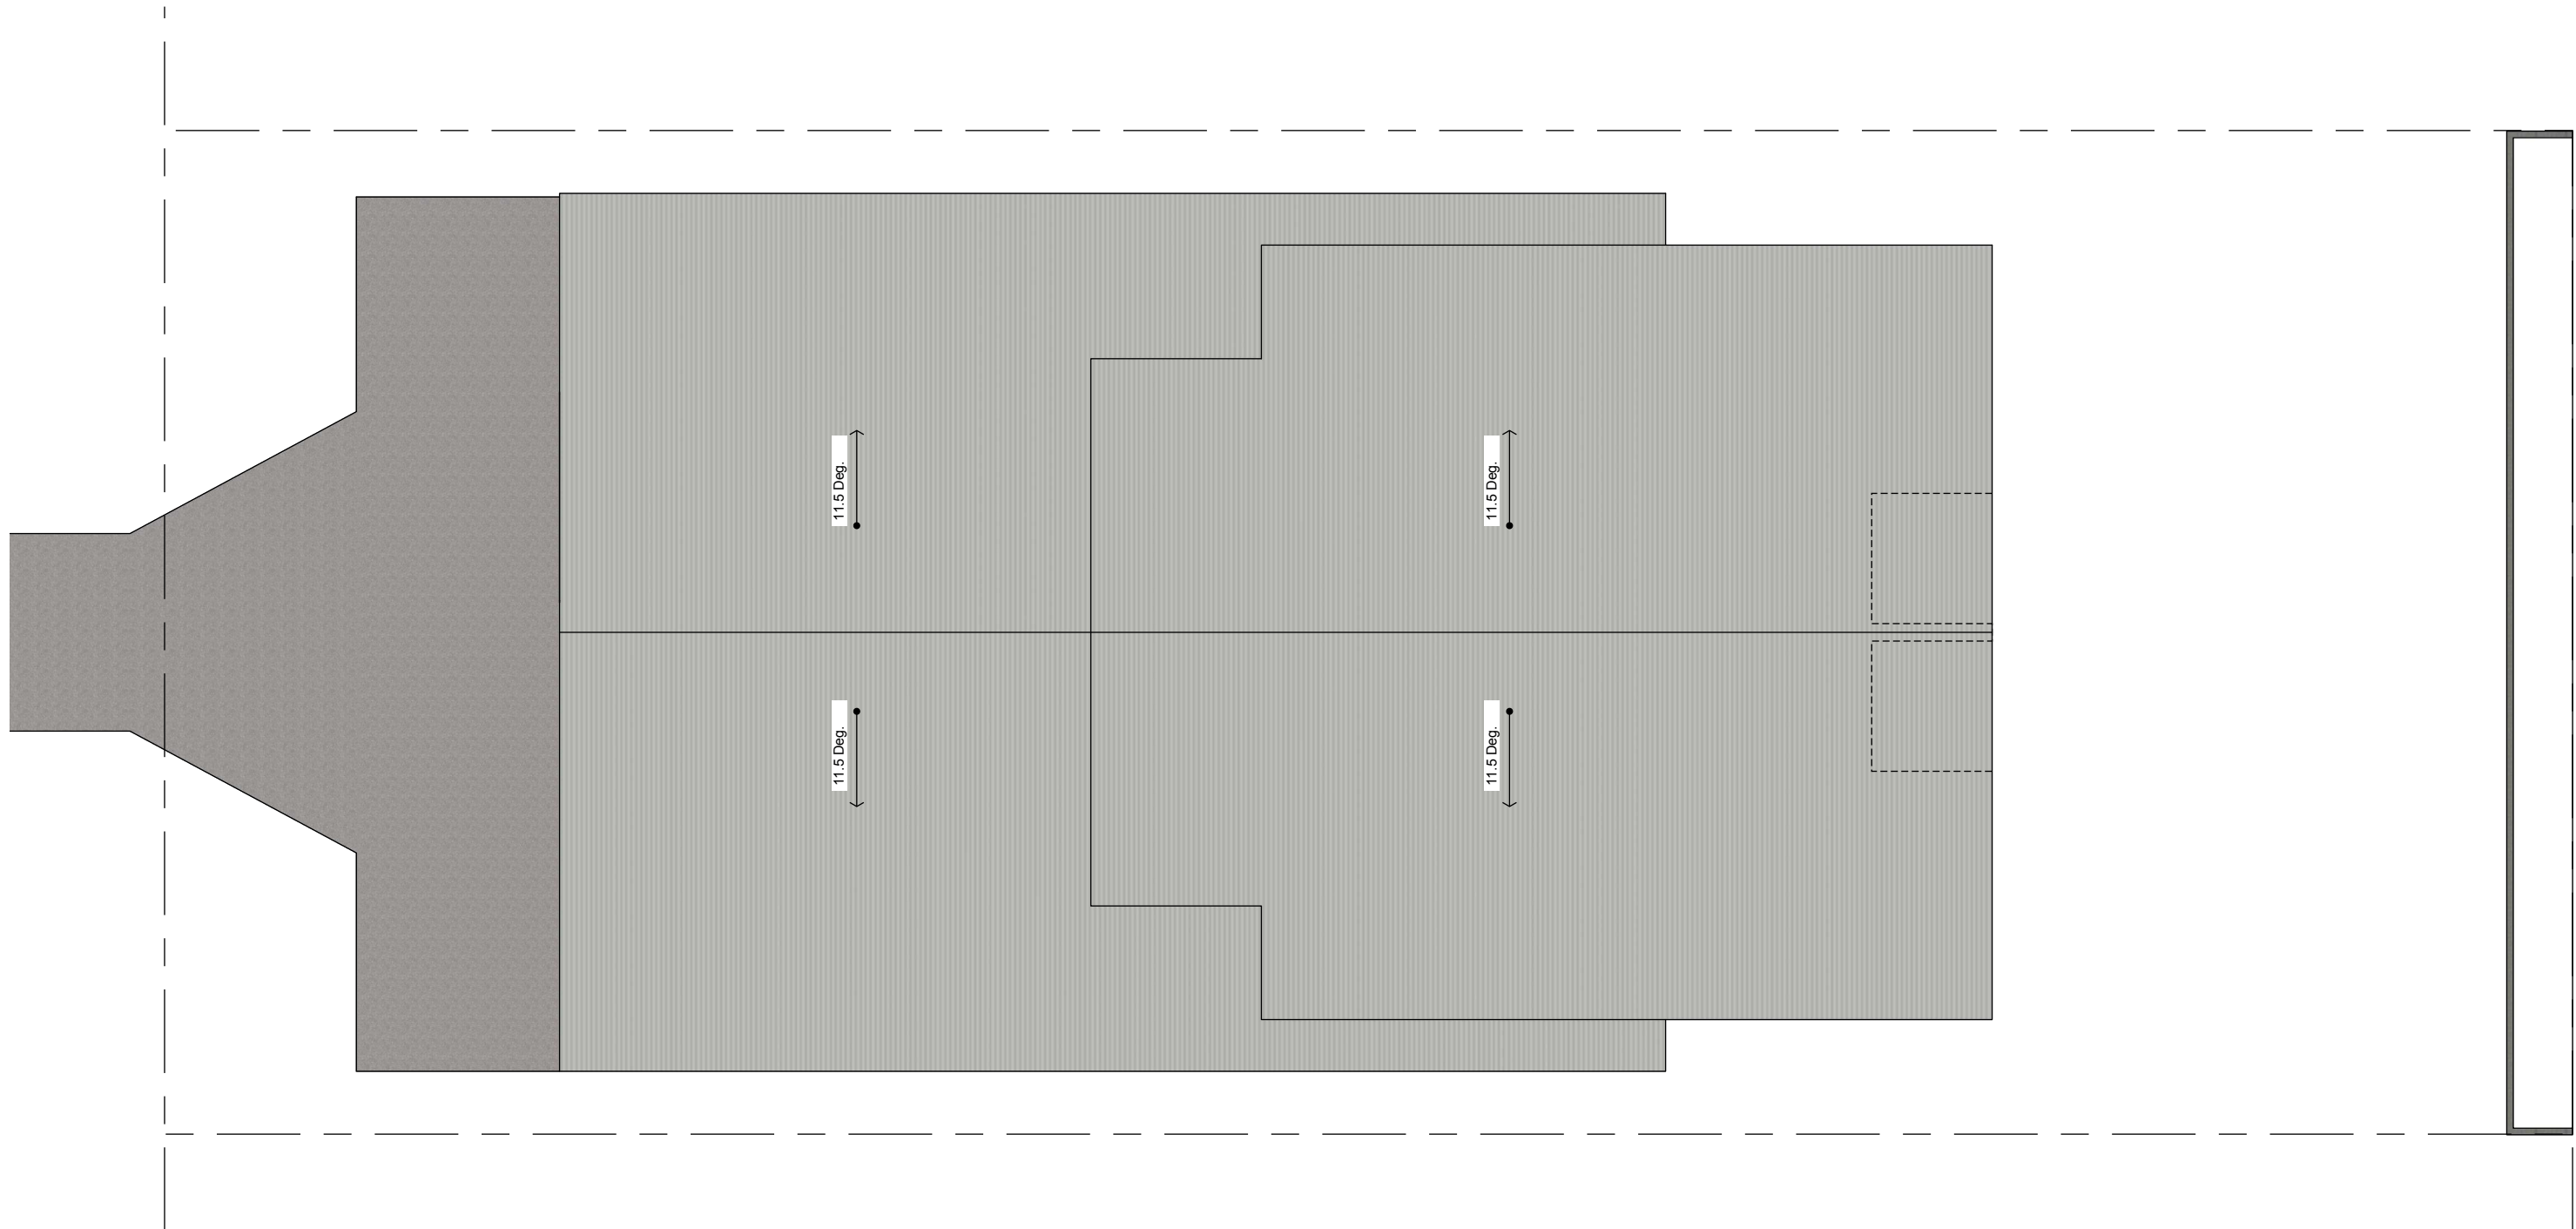

BUILDING DESIGNER
Redson Group Pty. Ltd.
trading as 'Progenia'
Wollongong, NSW 2500
E: contactus@progenia.com.au
A.B.N 21 158 799 663



Do not scale drawings. Use
figured dimensions only.
Check and verify levels and
dimensions on site prior to
commencement of any work,
the preparation of shop
drawings or the fabrication of
components.

This drawing is the copyright of
Redson Group Pty. Ltd. (Progenia) and
is protected under the Copy Right Act
1968. Do not alter, reduce or transmit in
any form or by any means without the
express permission of Redson Group
Pty. Ltd. (Progenia).


CLIENT
Brett McCroary
PROJECT
Proposed Dual Occupancy
LOCATION
37 Osborne St Gerringong NSW
PROJECT NUMBER
#038.2020

REVISION	DRAWN BY	DATE
1	JL	02.07.21

Issued for DA

DESCRIPTION	PAGE SCALE	PAGE SIZE
Roof Plan	1 : 100	A3

A-300

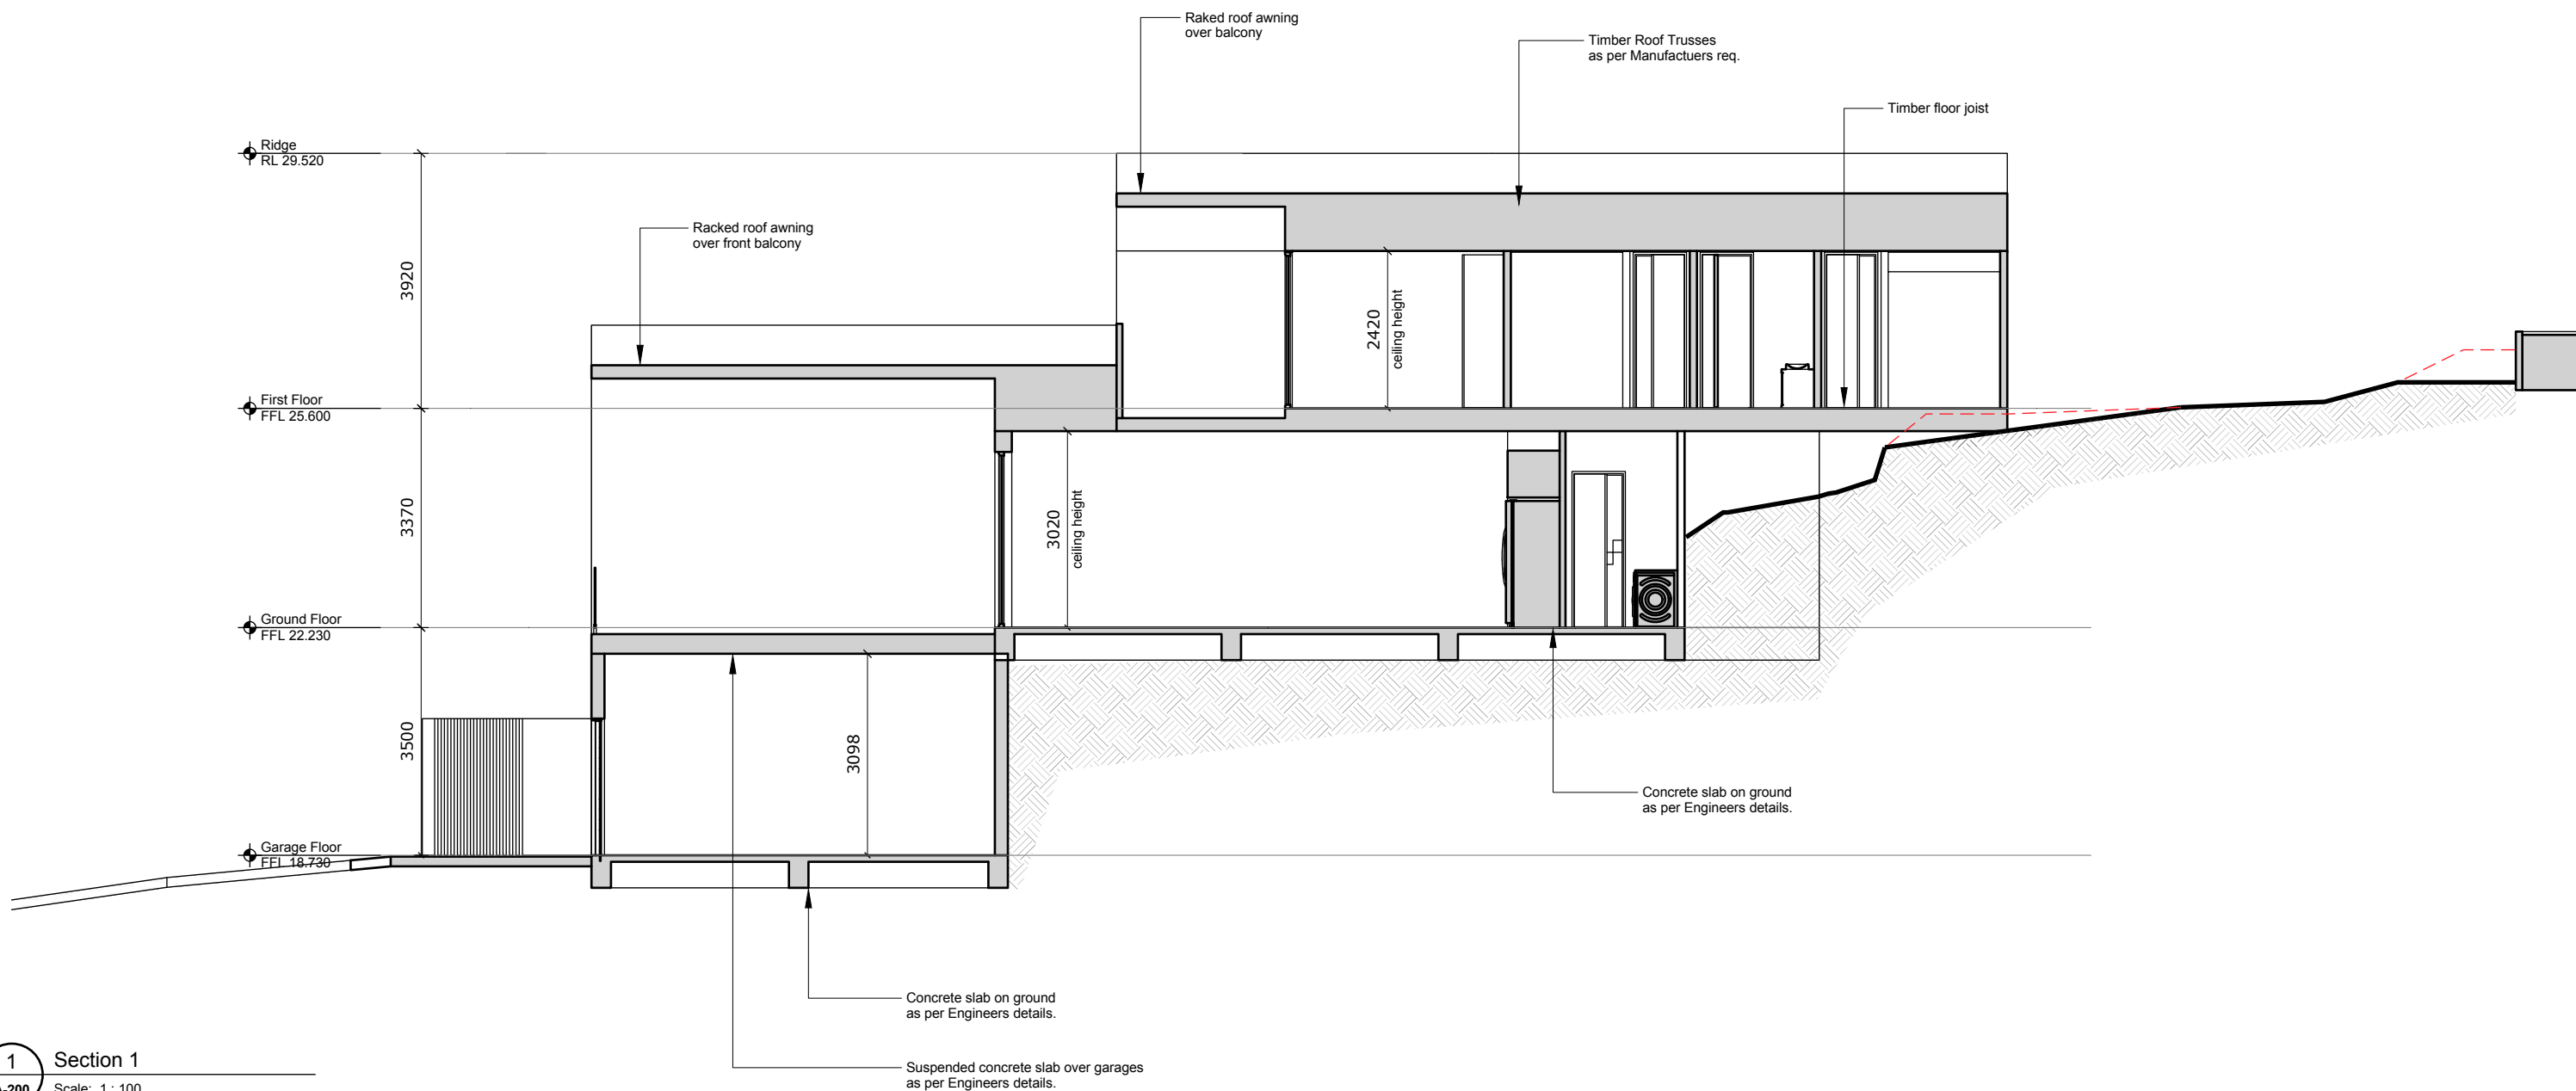

1 Section 1
A-200 Scale: 1 : 100